

A-2

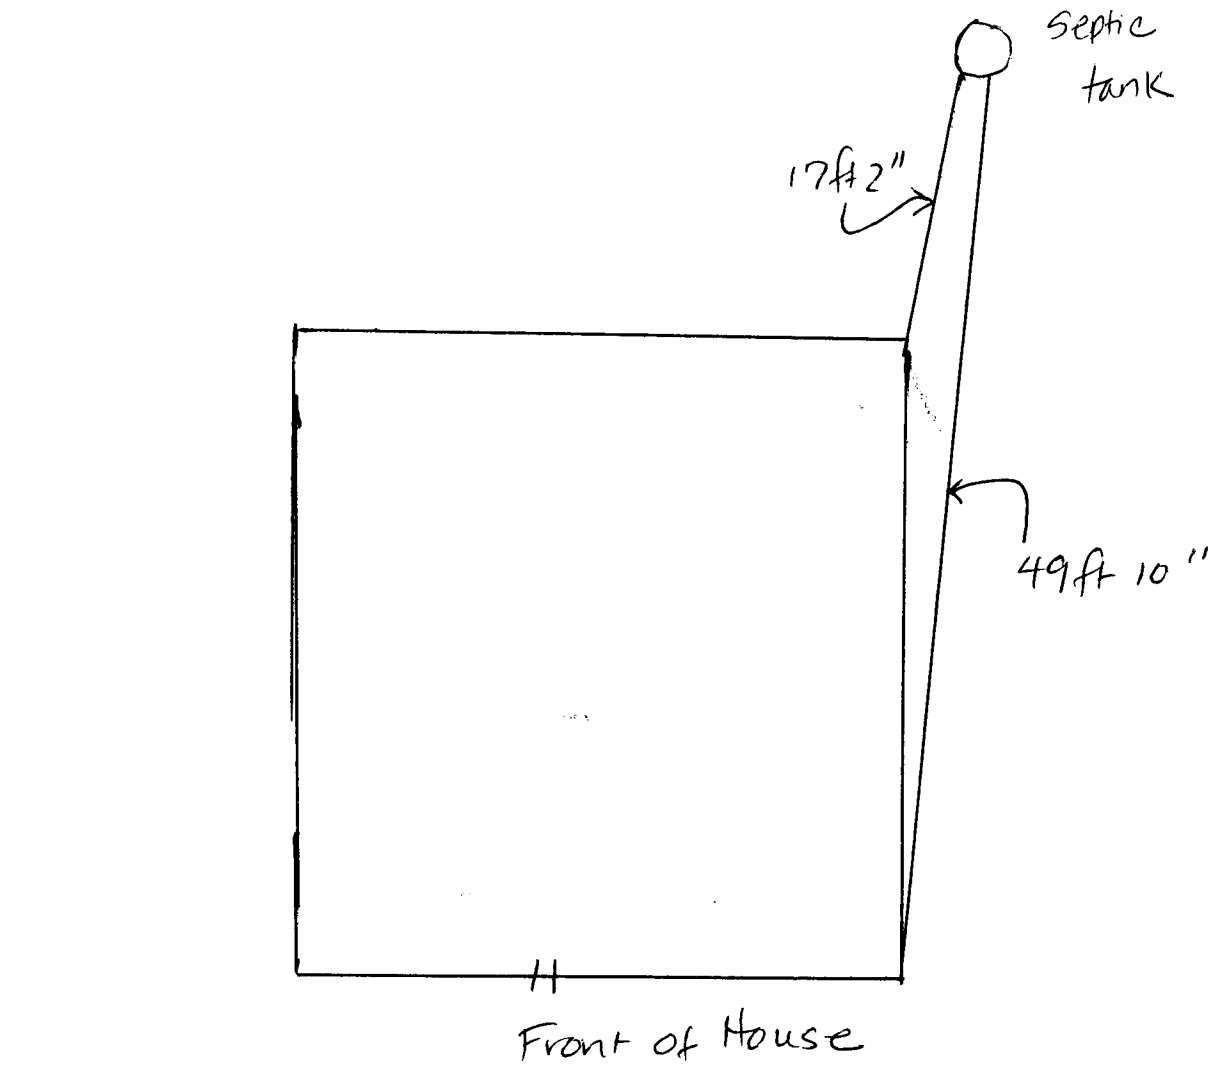


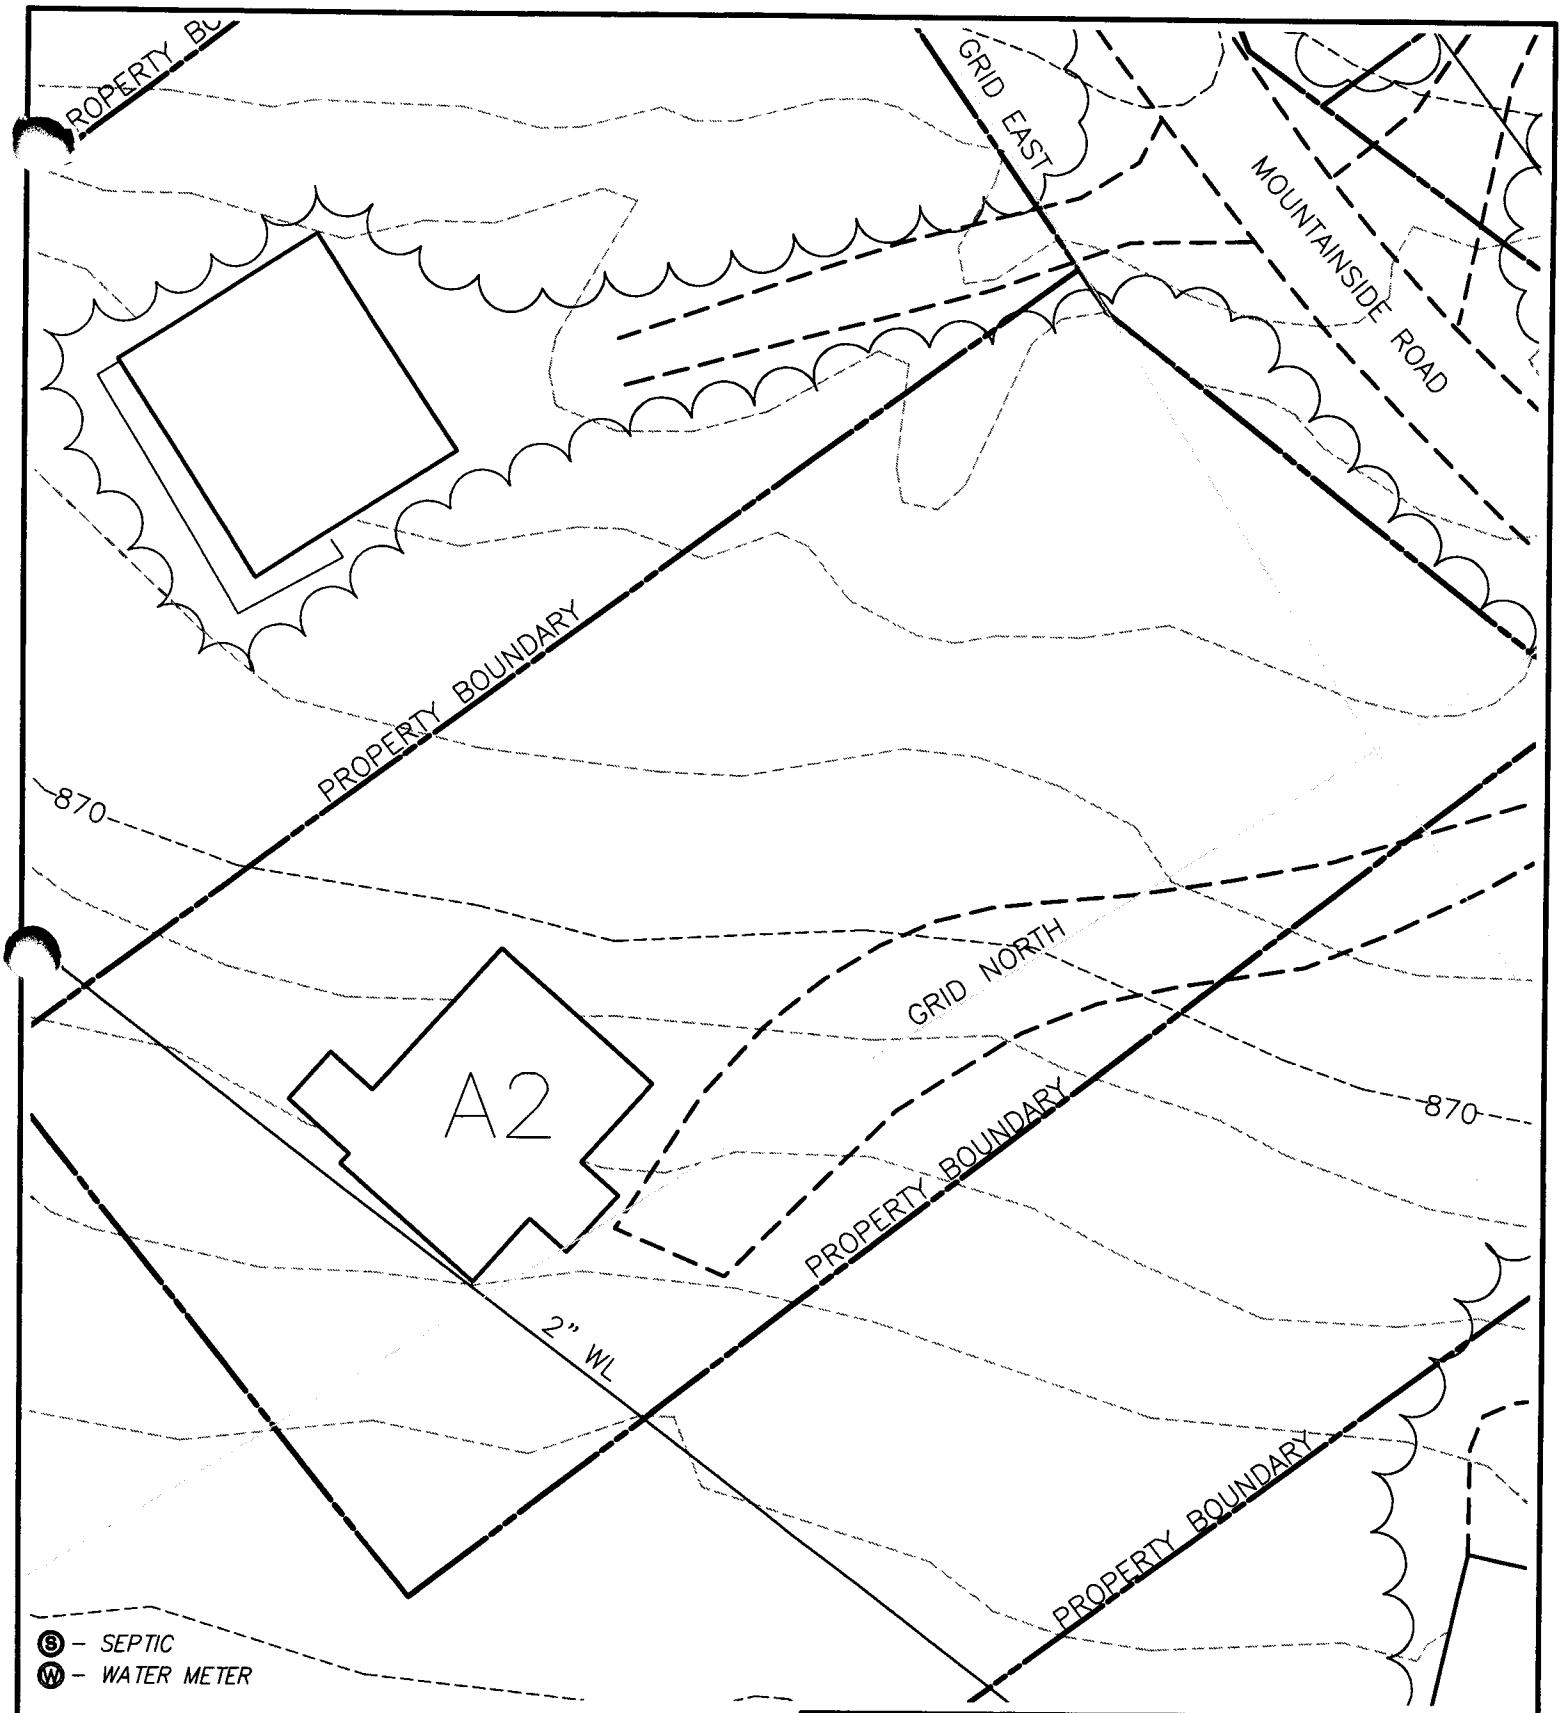

NOTE:
1. Property lines and utilities are shown in an approximated location.

1225 MOUNTAINSIDE ROAD
SECTION A–LOT 2
UTILITY LOCATION MAP


SURVEY: PAS	C.I.: 2'
DRAWN BY: P–L	JOB NO.: 0902011
SCALE: SHOWN	DATE: 9/9/11
SHEET:	A2

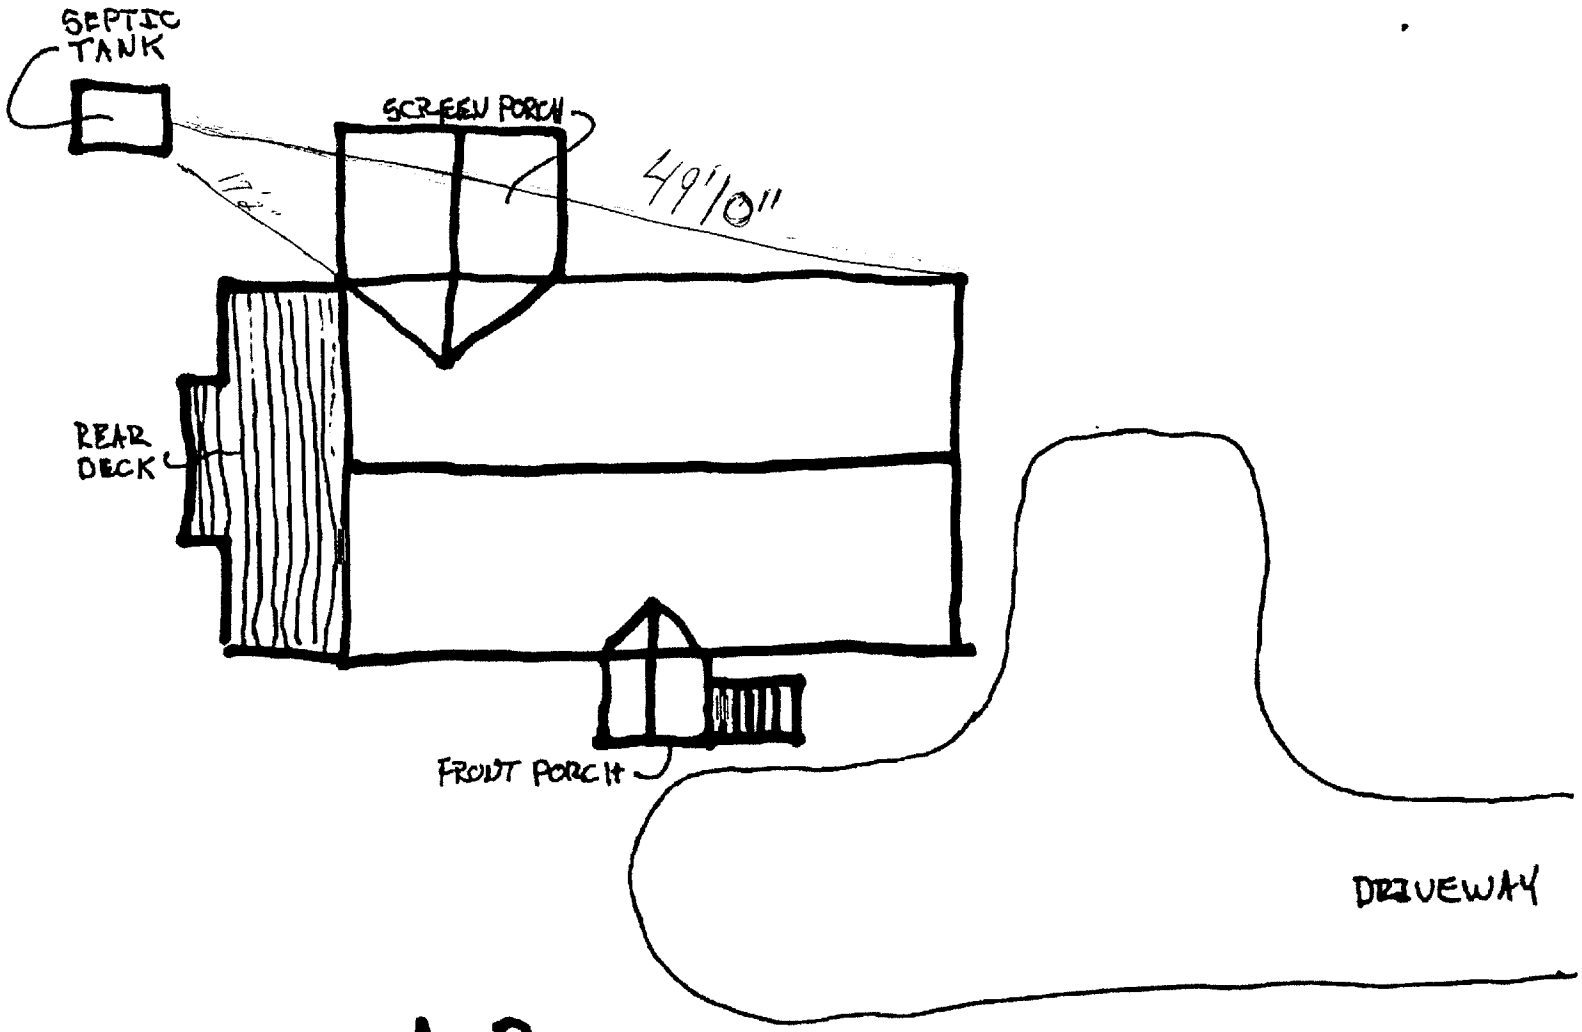

A-2

Scanned with CamScanner

MOUNTAINSIDE ROAD

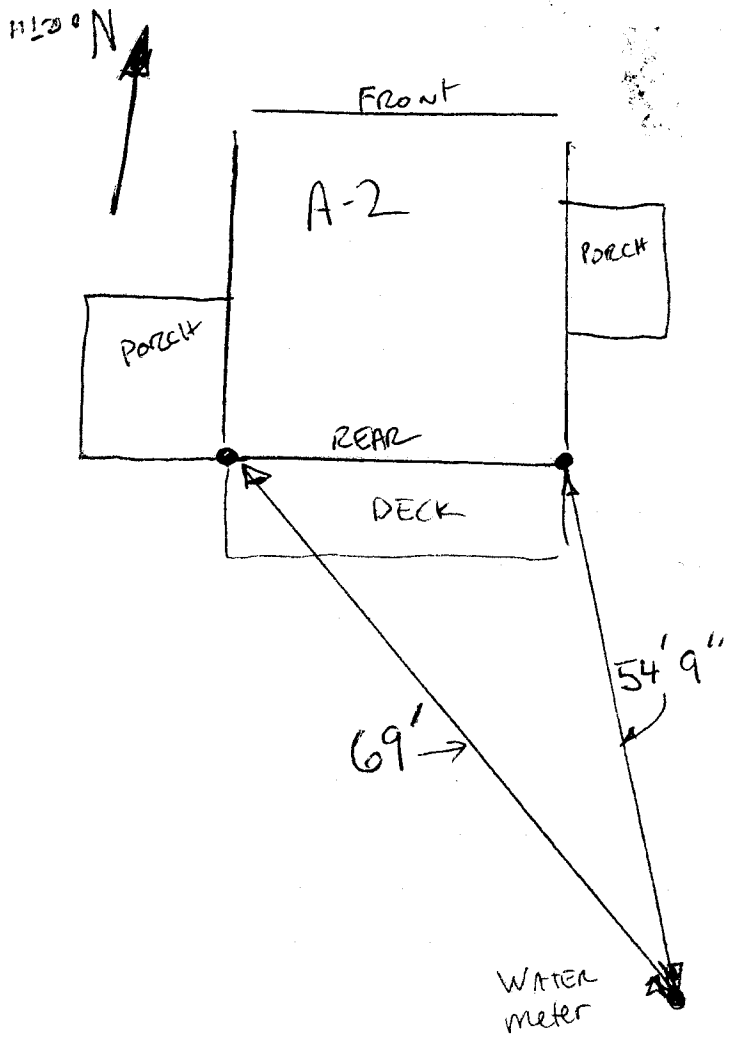

BLUEBIRD LANE