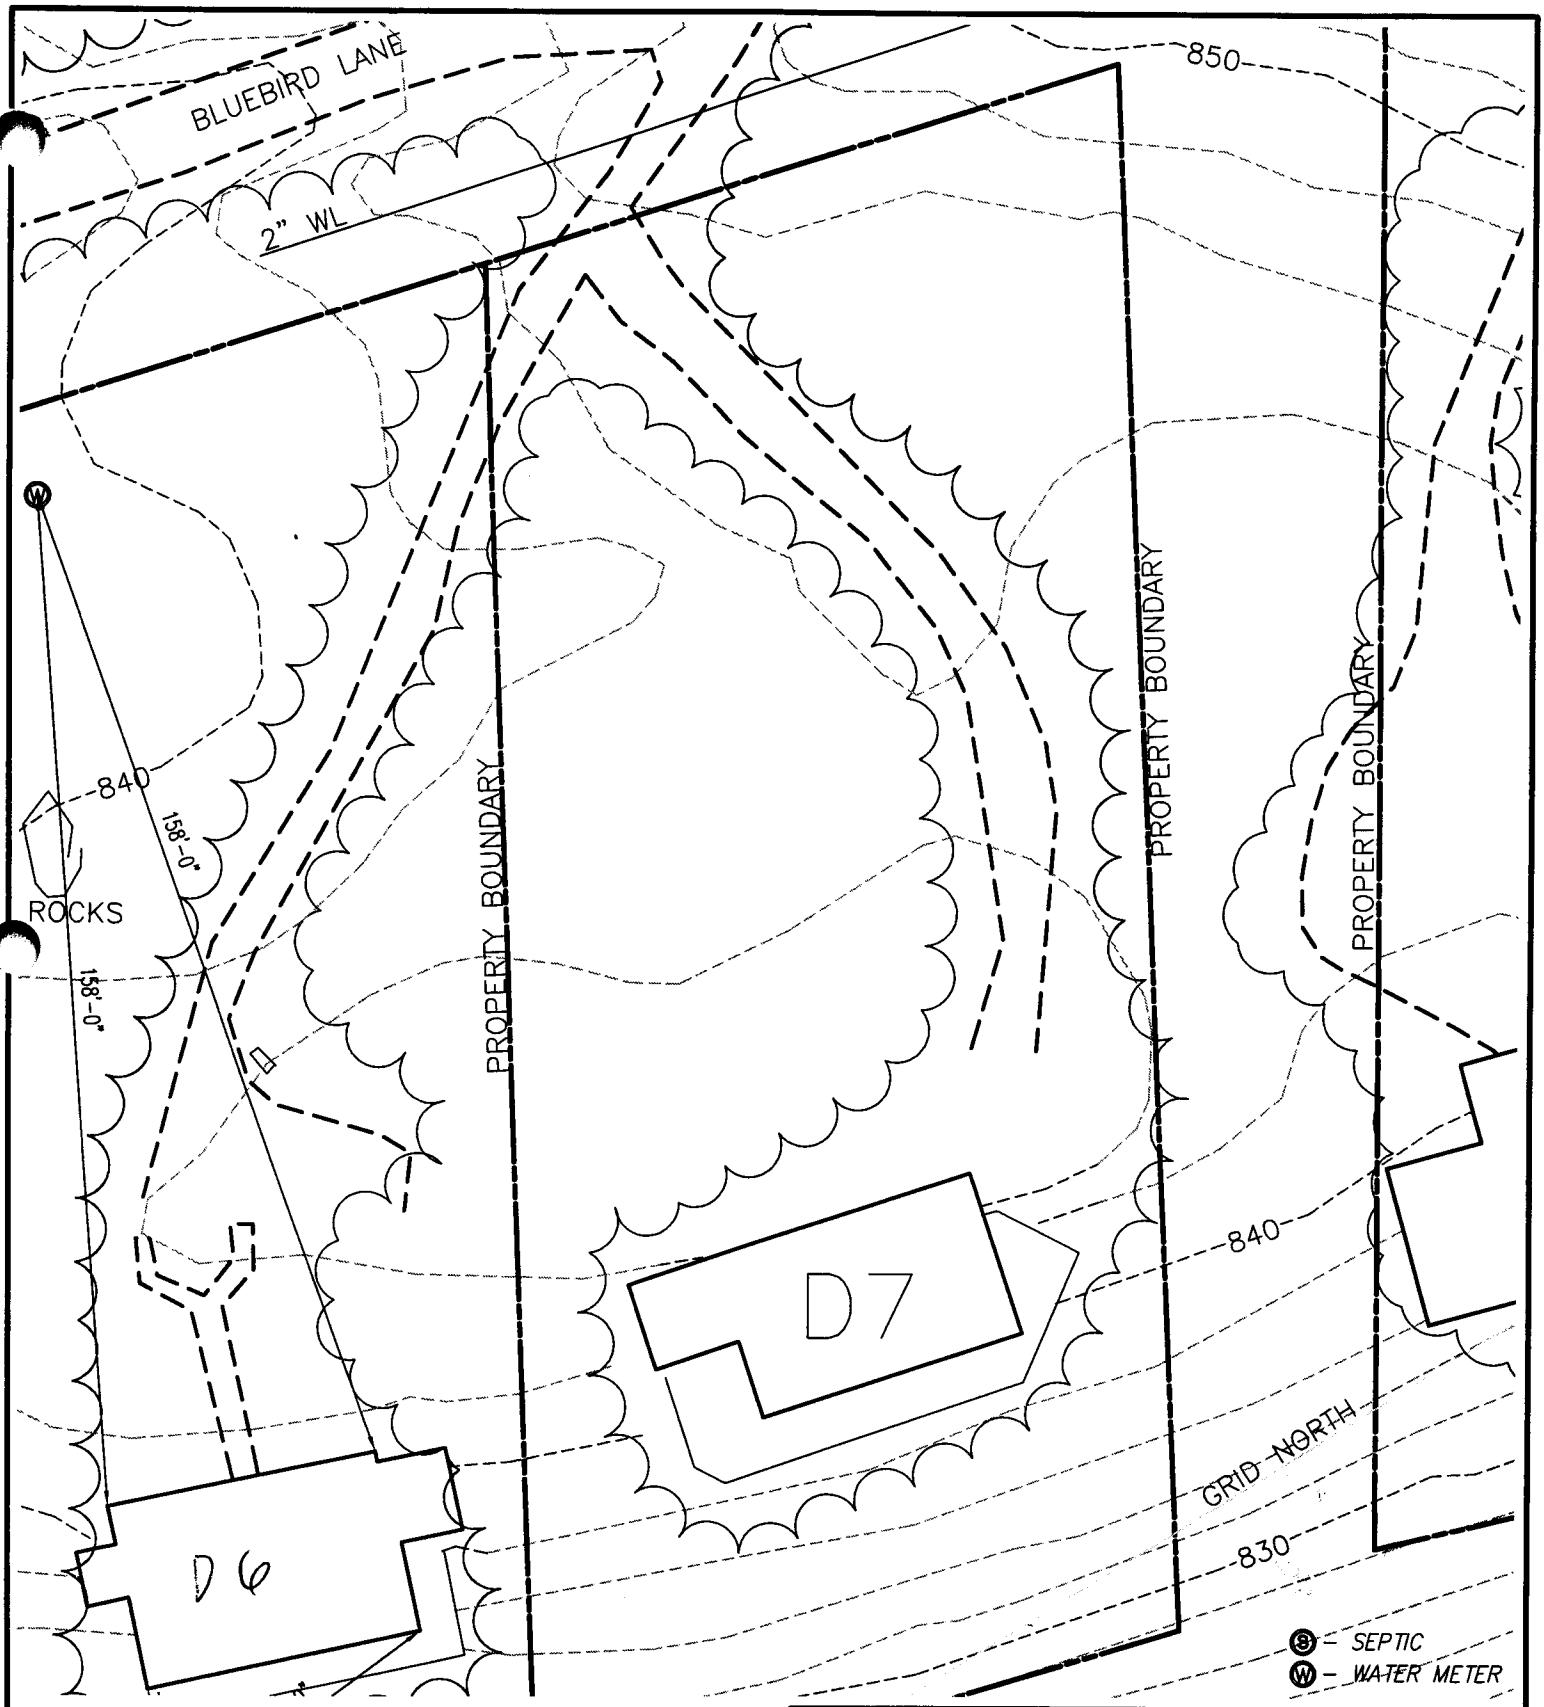


30 0 30

Scale 1" = 30 ft


NOTE:
1. Property lines and waterline are shown in an approximated location.

87 BLUEBIRD LANE
SECTION D–LOT 7
UTILITY LOCATION MAP

SURVEY: PAS	C.I.: 2'
DRAWN BY: P–L	JOB NO.: 0902011
SCALE: SHOWN	DATE: 9/9/11
SHEET:	D7

C-25

COLD RUN VALLEY ROAD

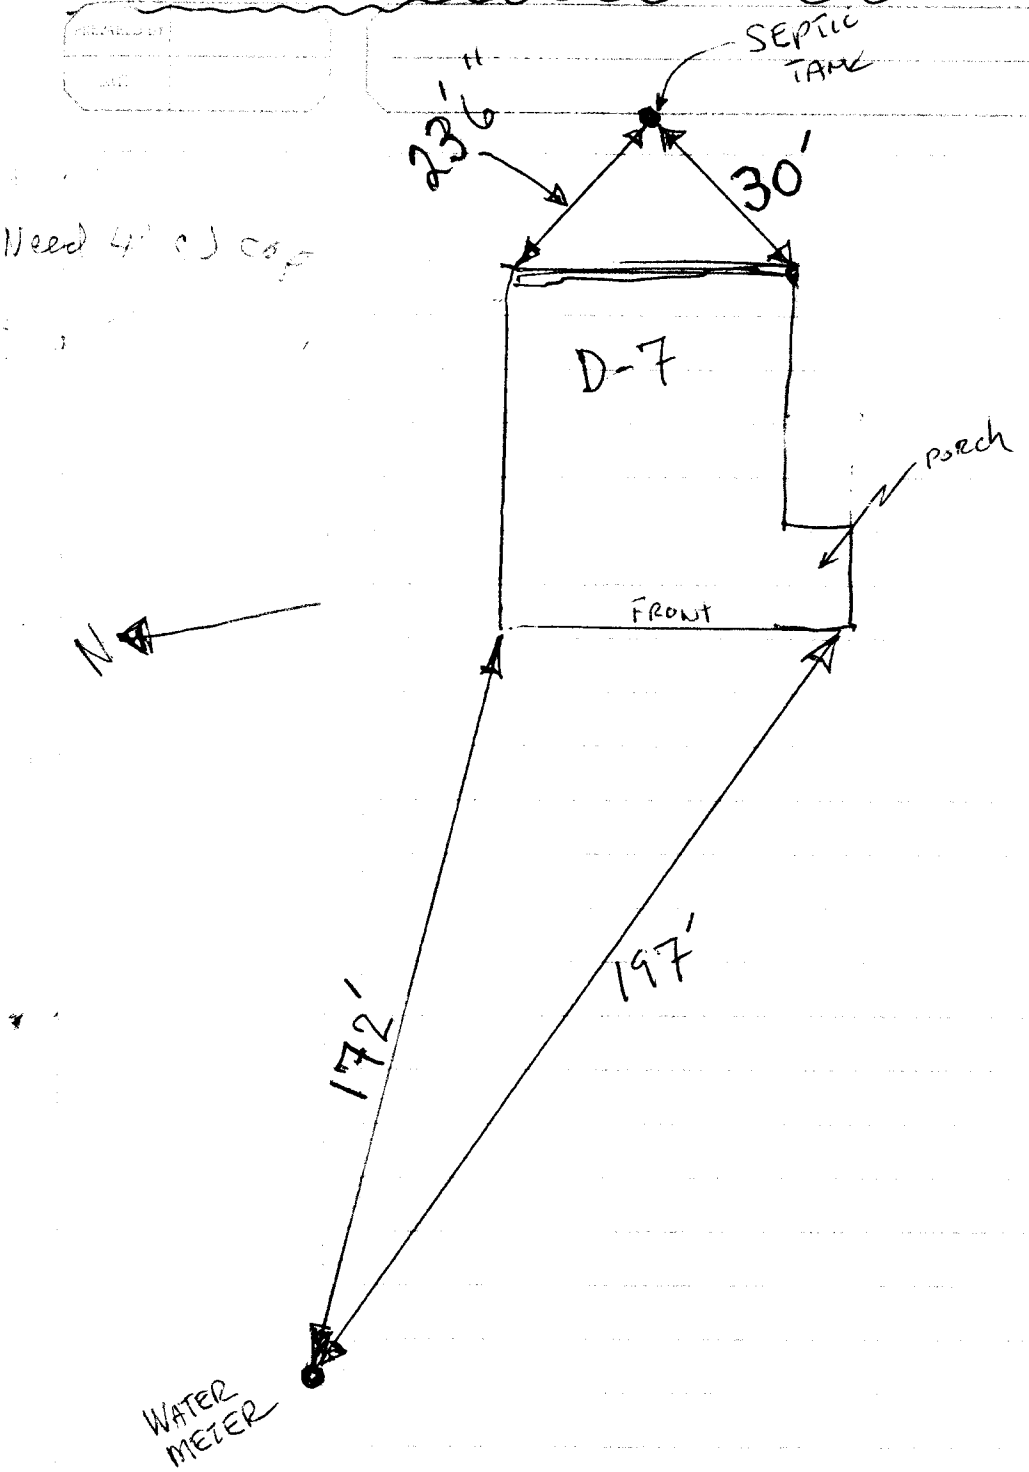

C-52

BLUEBIRD LANE