
G-1.


1999

2 TANKS
above ground
Level

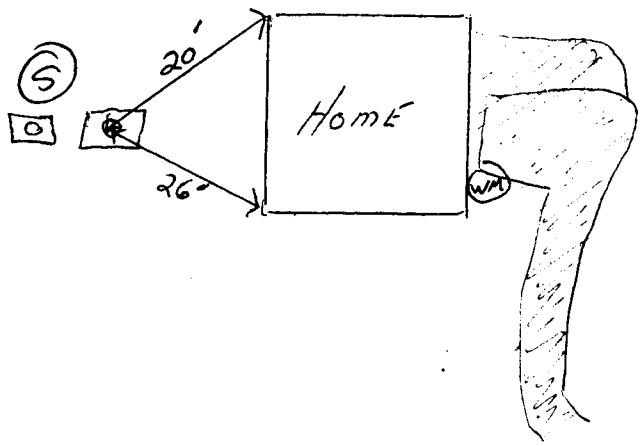


G-2

1999

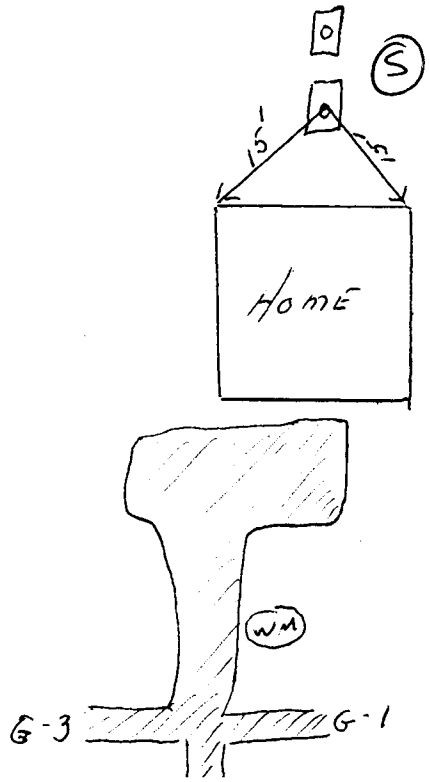


2 Tanks
above ground
Level

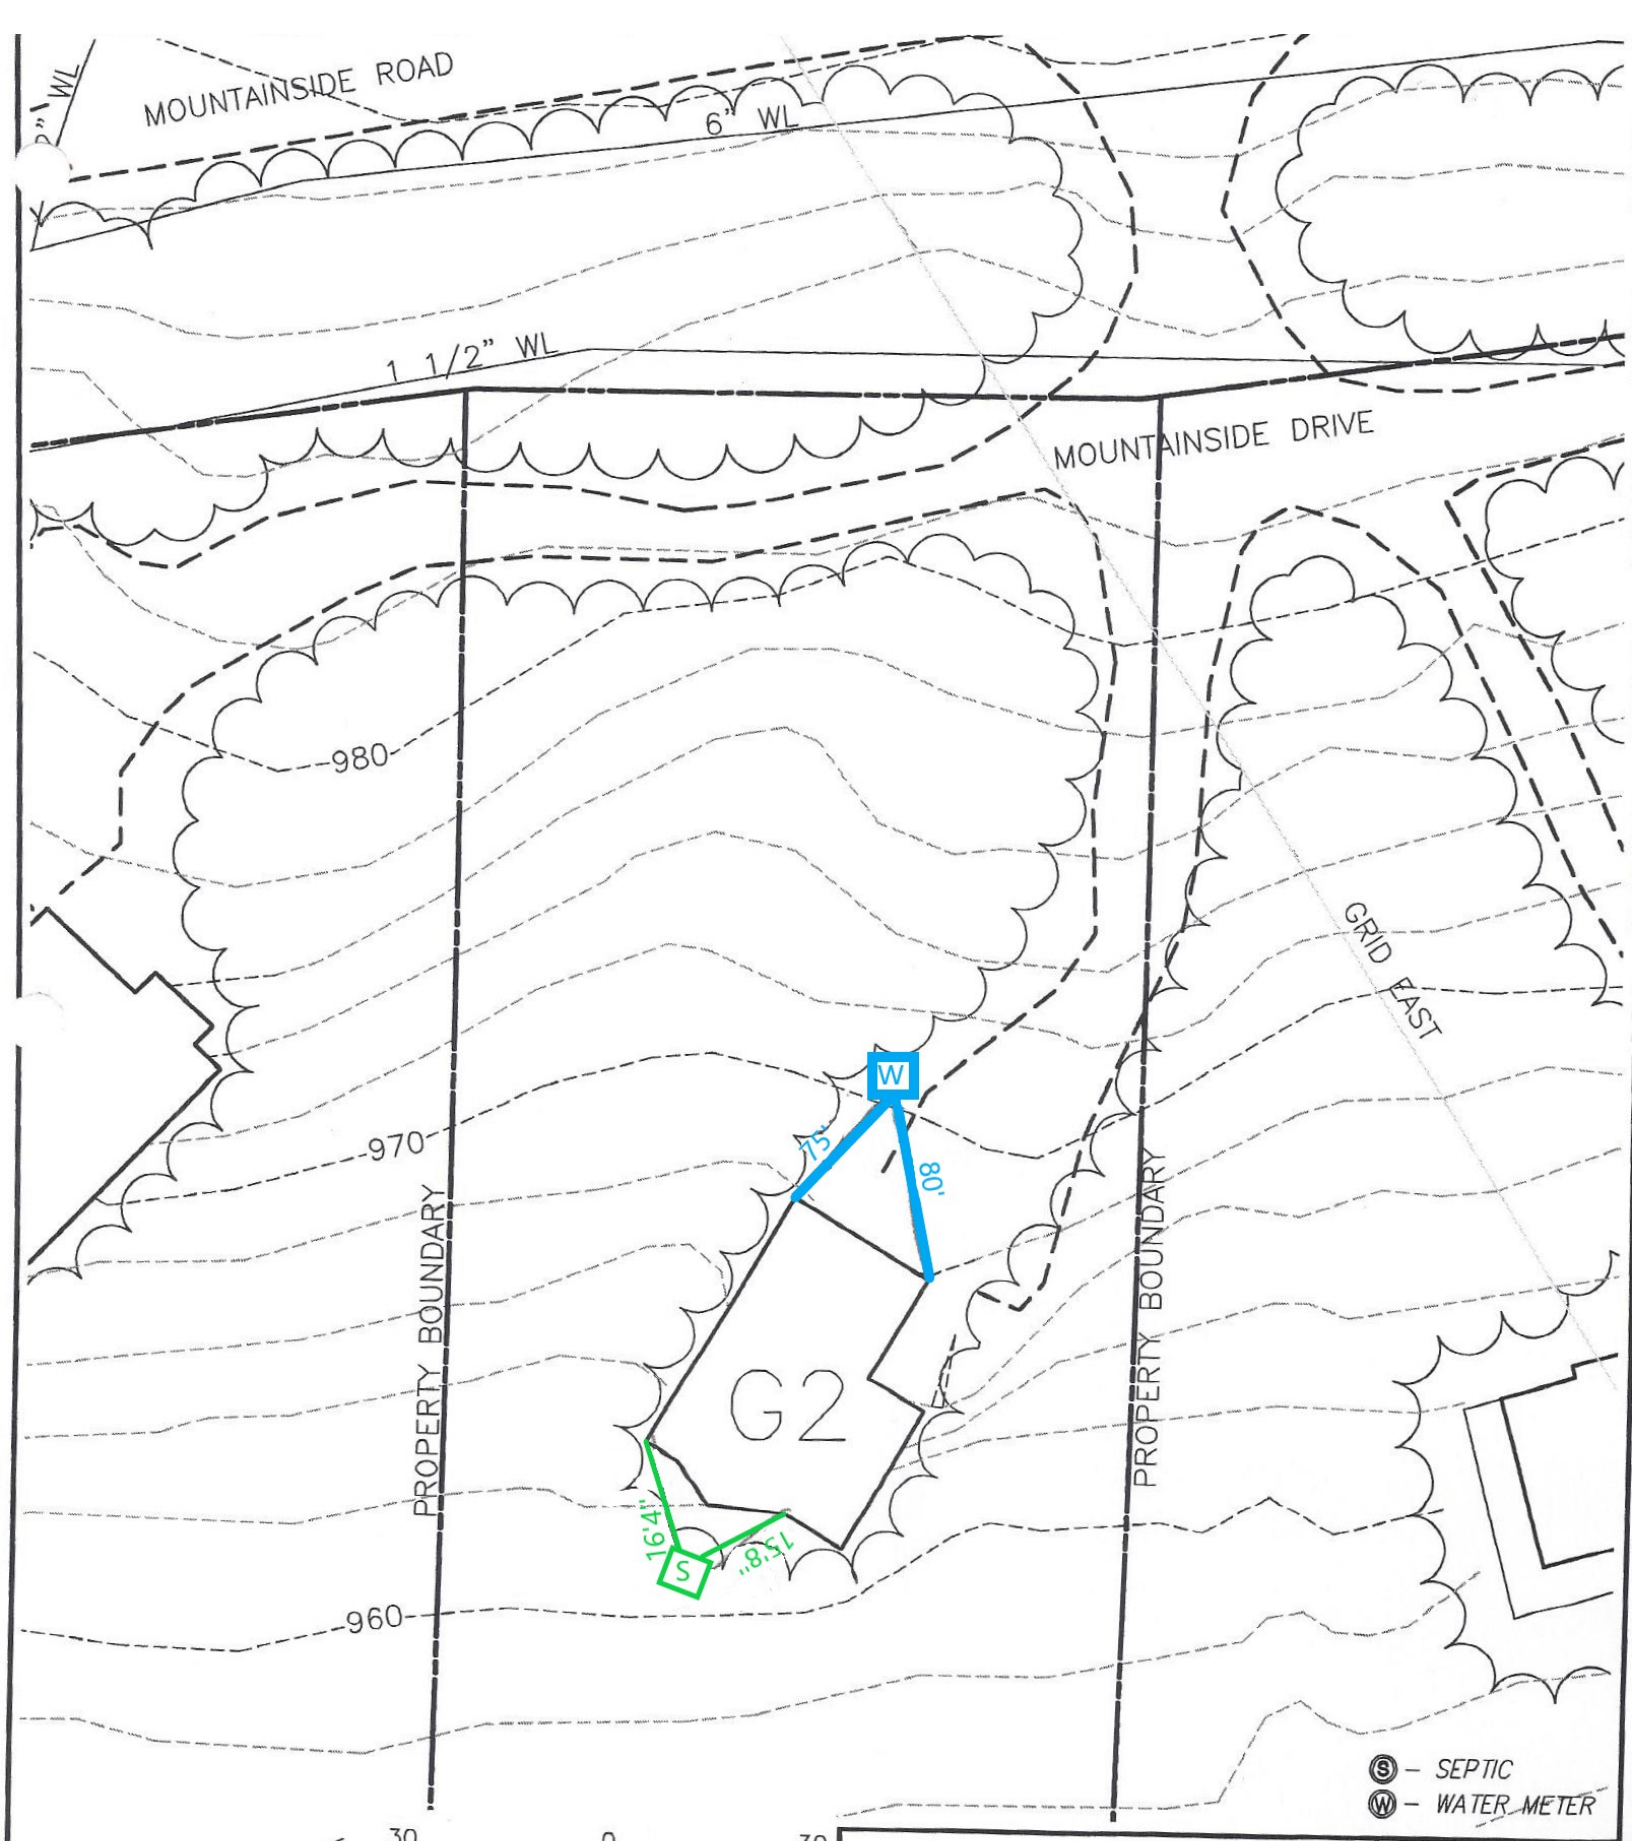

NOTE:
1. Property lines and utilities are shown in an approximated location.

13 MOUNTAINSIDE DRIVE SECTION G–LOT 2 UTILITY LOCATION MAP

SURVEY: PAS	C.I.: 2'
DRAWN BY: P–L	JOB NO.: 0902011
SCALE: SHOWN	DATE: 9/9/11
SHEET:	G2

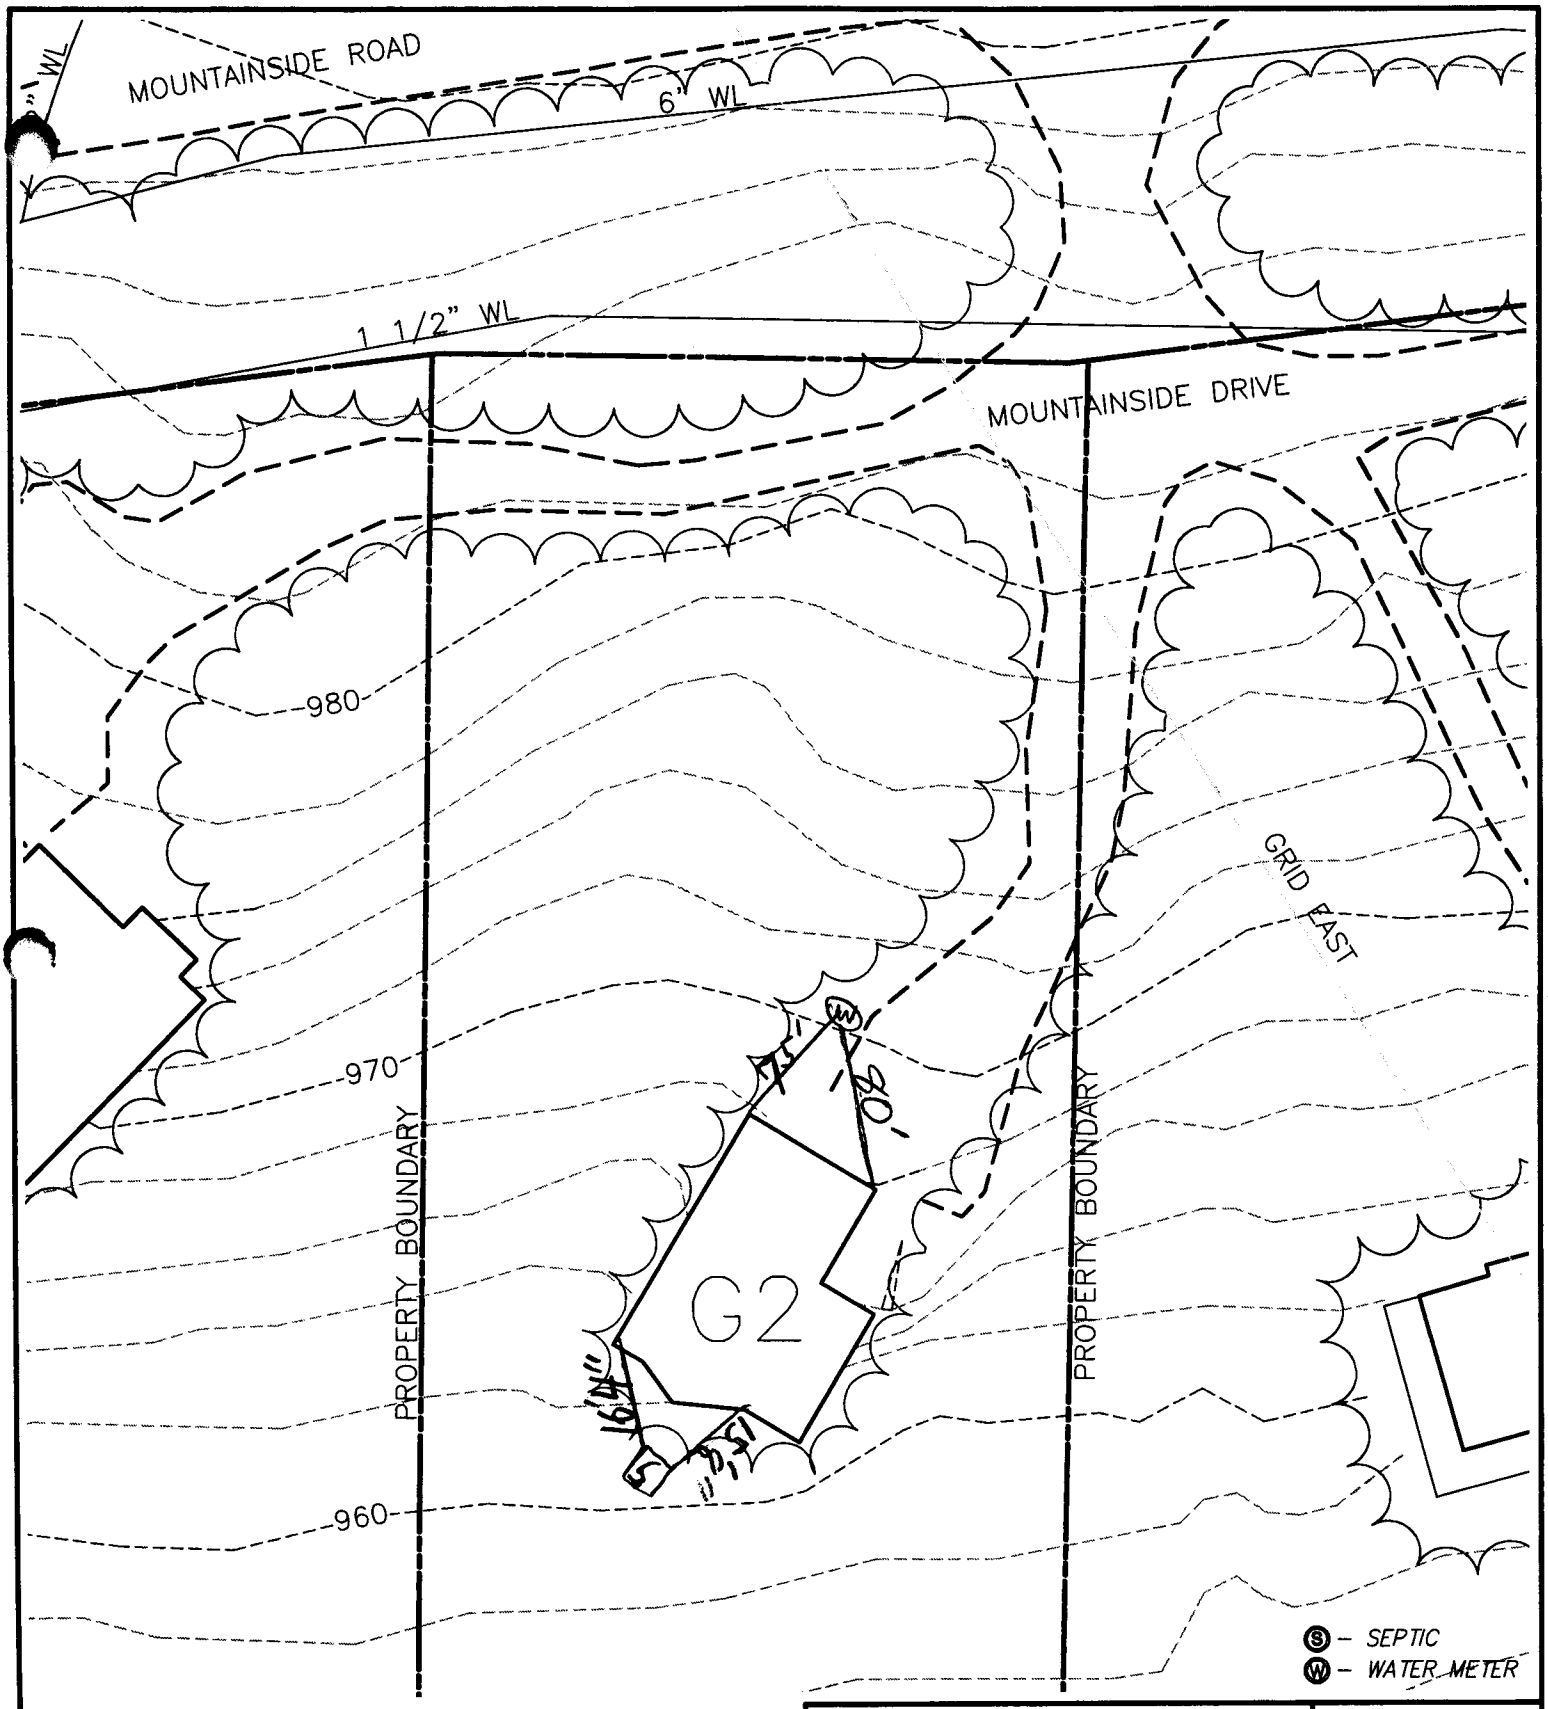

30 0 30

Scale 1" = 30 ft

NOTE:
1. Property lines and utilities are shown in an approximated location.

13 MOUNTAINSIDE DRIVE SECTION G–LOT 2 UTILITY LOCATION MAP

SURVEY: PAS	C.I.: 2'
DRAWN BY: P–L	JOB NO.: 0902011
SCALE: SHOWN	DATE: 9/9/11
SHEET:	G2