

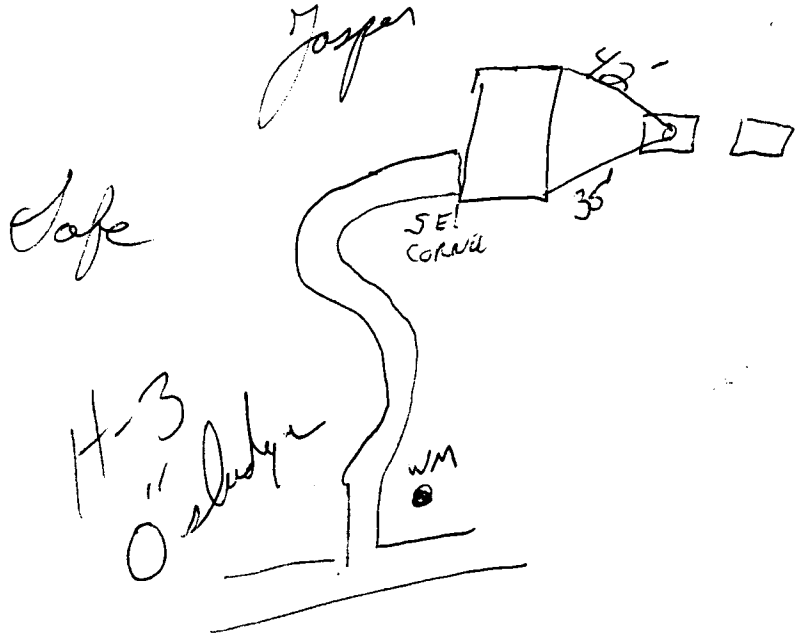


25
17
4:12

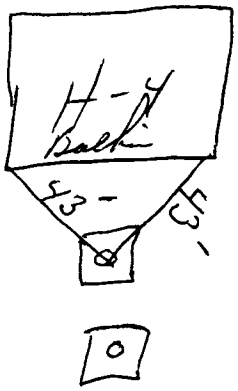

John Jobs March
2005

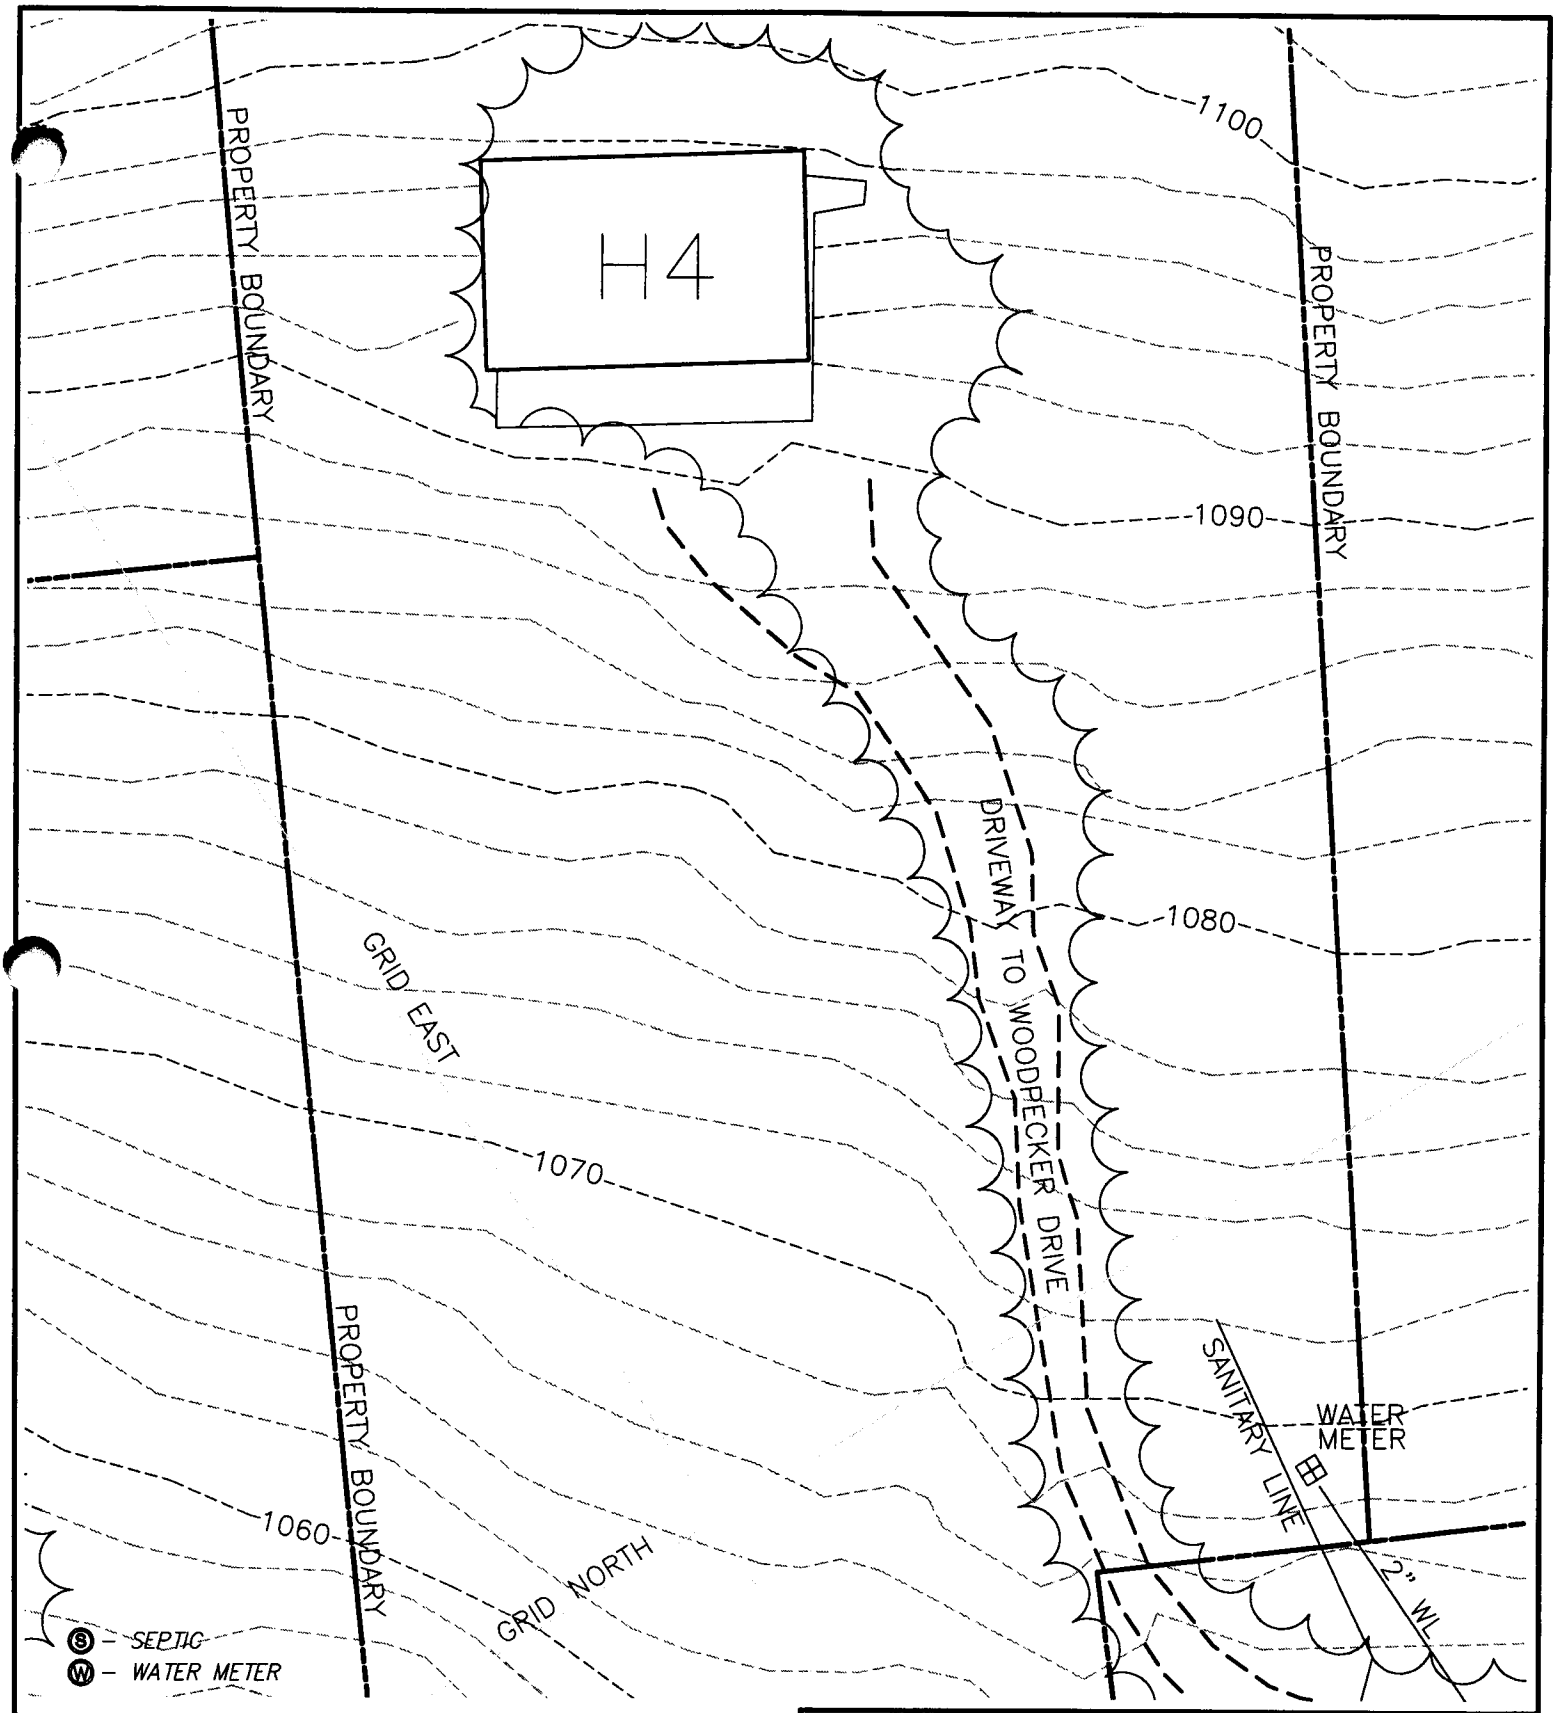


NOTE:
1. Property lines and utilities are shown in an approximated location.

155 WOODPECKER DRIVE
SECTION H–LOT 4
UTILITY LOCATION MAP

SURVEY: PAS	C.I.: 2'
DRAWN BY: P–L	JOB NO.: 0902011
SCALE: SHOWN	DATE: 9/9/11
SHEET:	H4

12-22

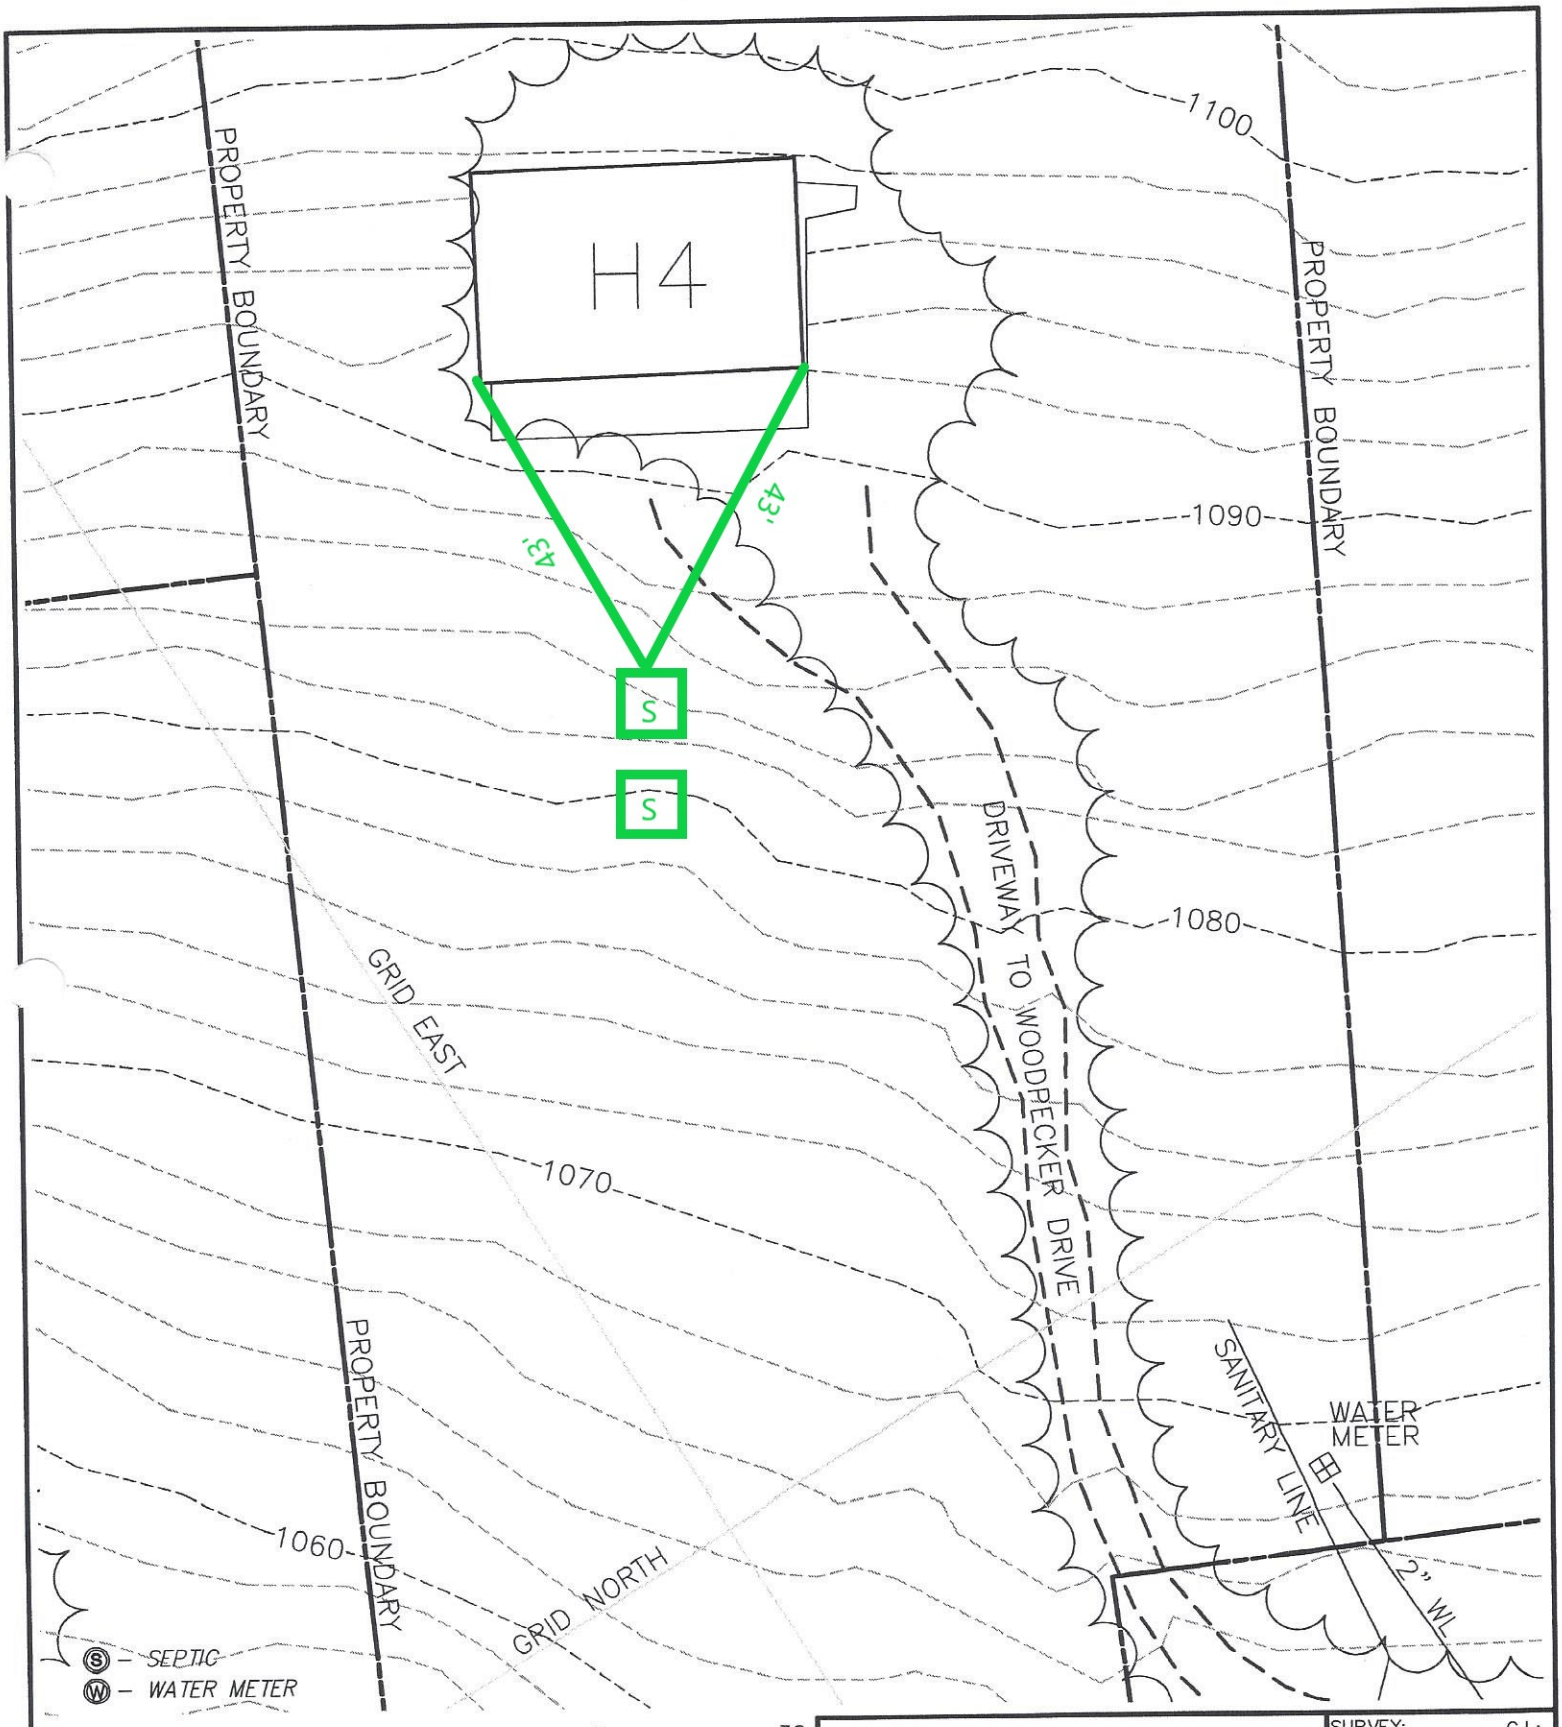

NOTE:
1. Property lines and utilities are shown in an approximated location.

155 WOODPECKER DRIVE
SECTION H–LOT 4
UTILITY LOCATION MAP

SURVEY: PAS	C.I.: 2'
DRAWN BY: P–L	JOB NO.: 0902011
SCALE: SHOWN	DATE: 9/9/11
SHEET:	H4

B-32