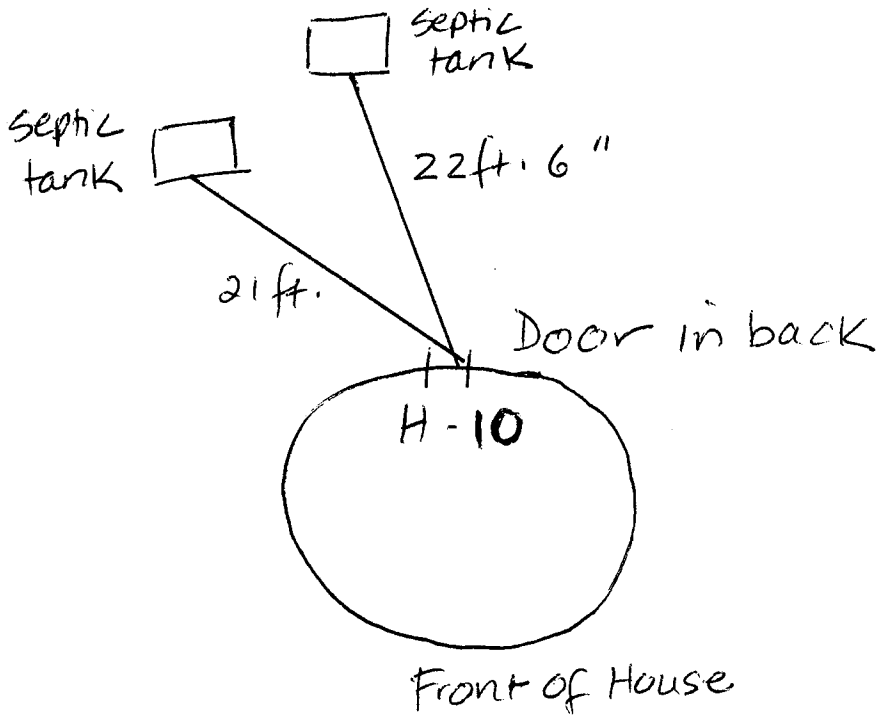
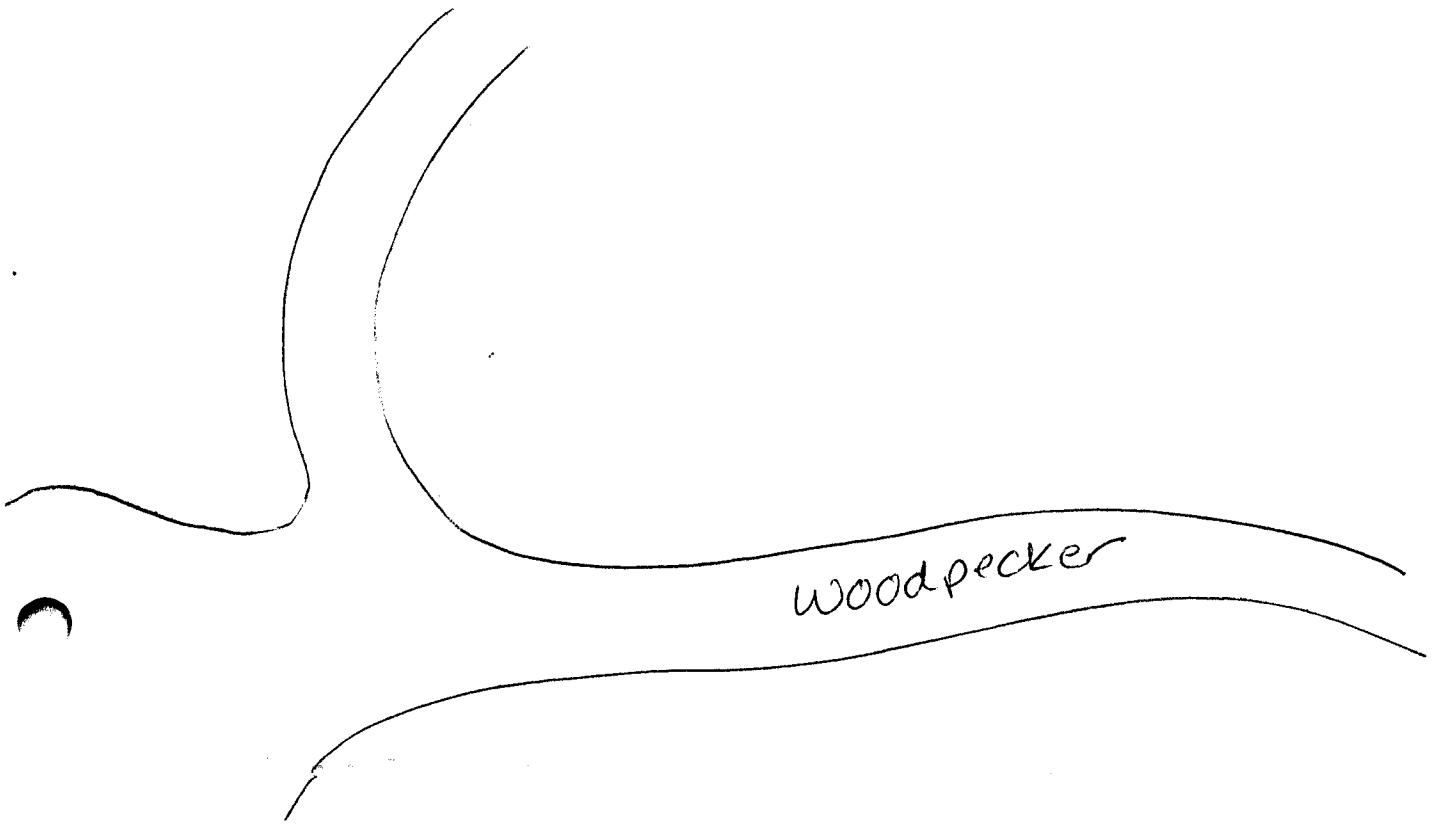
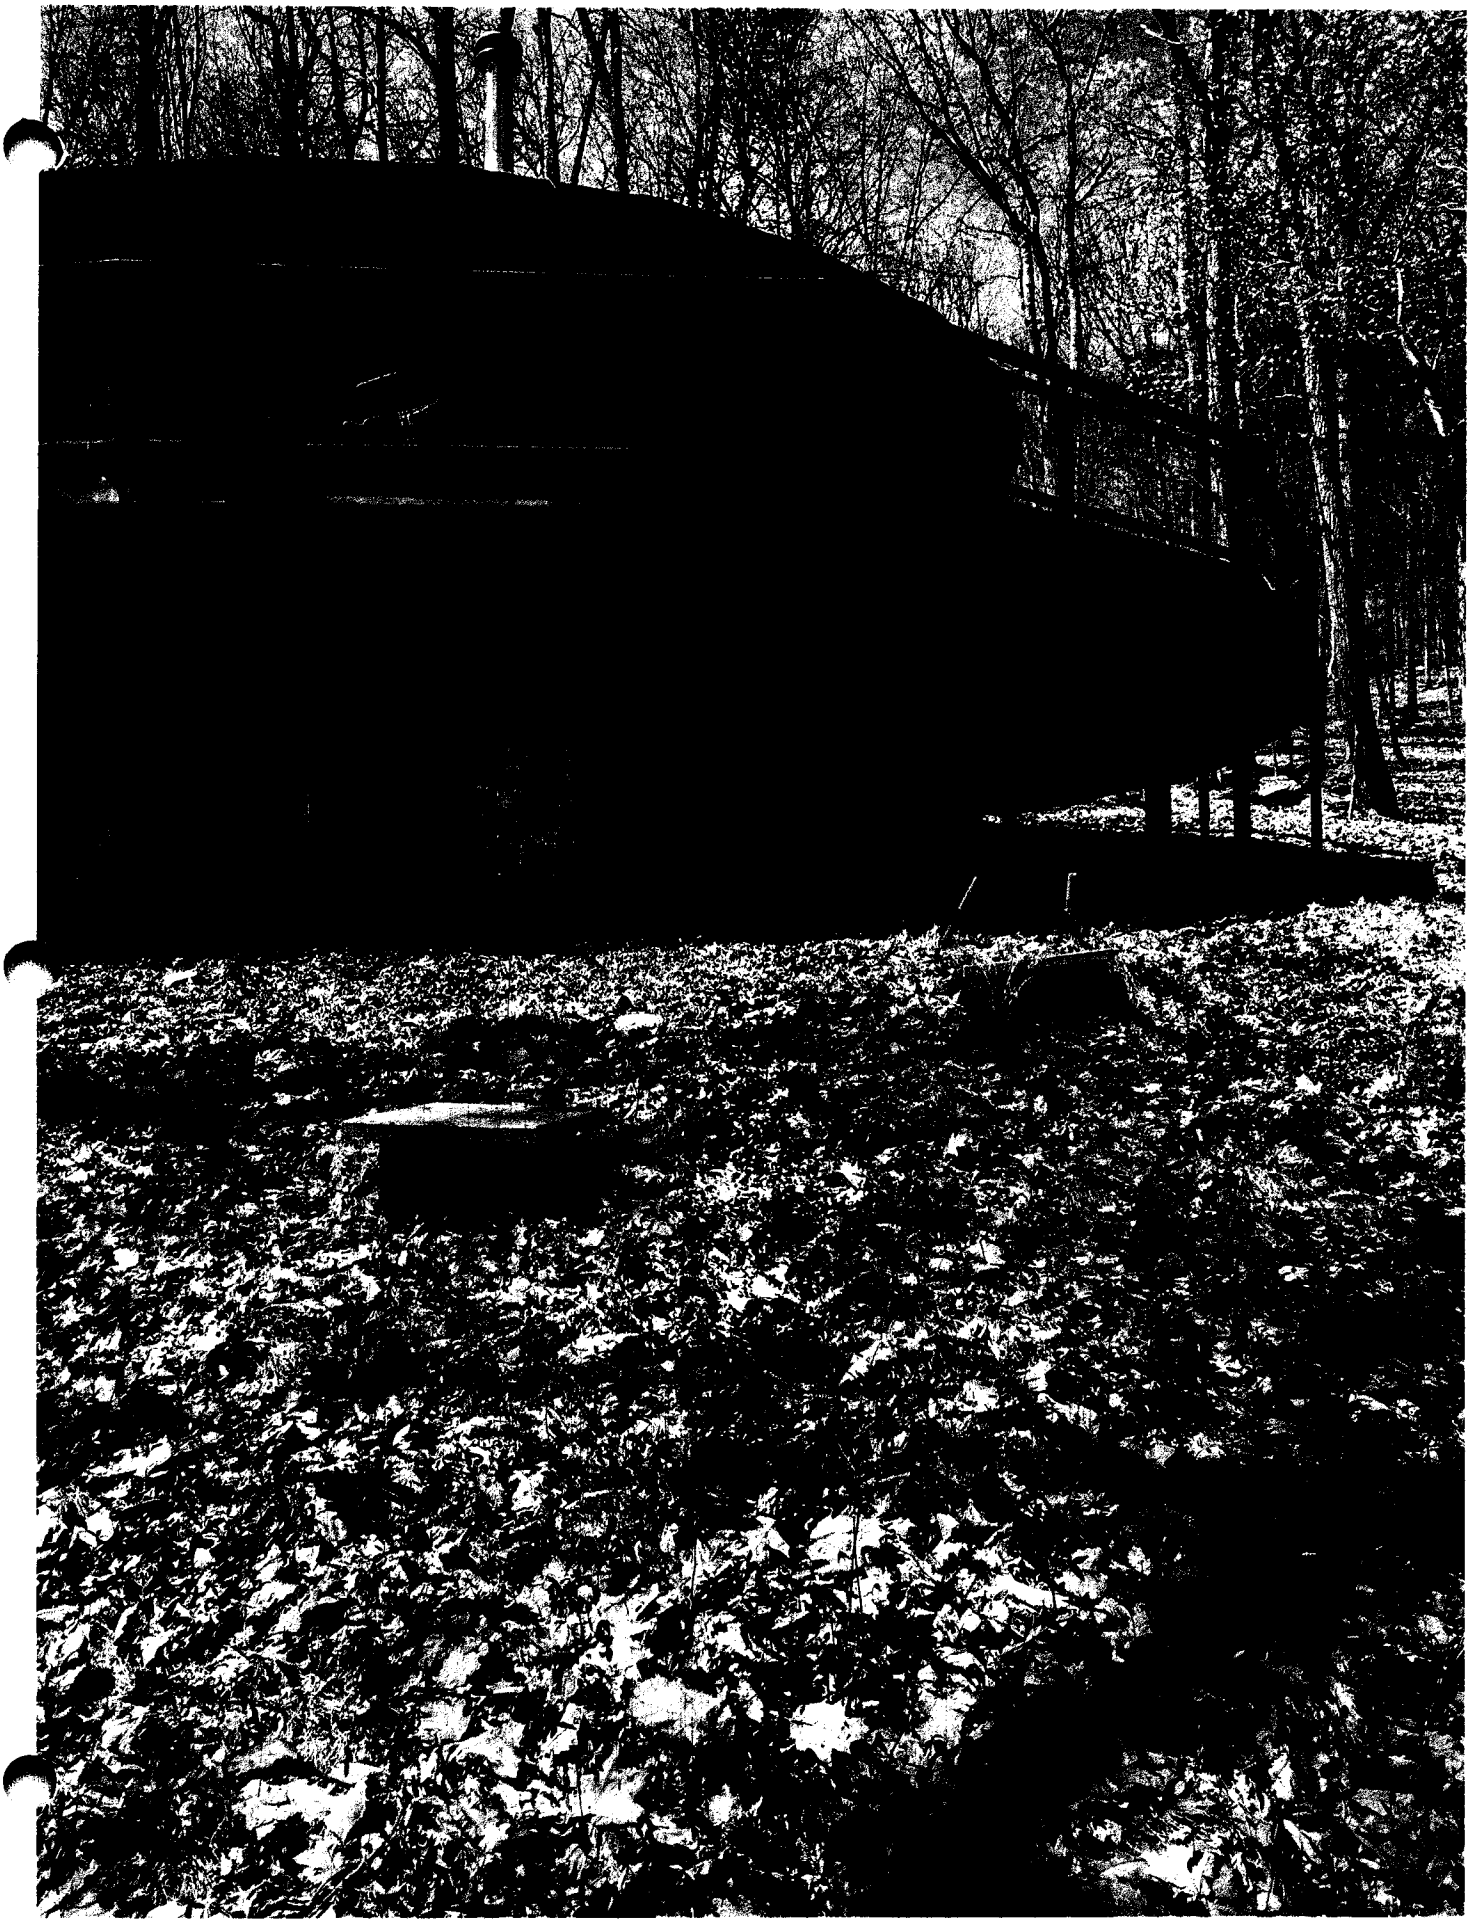
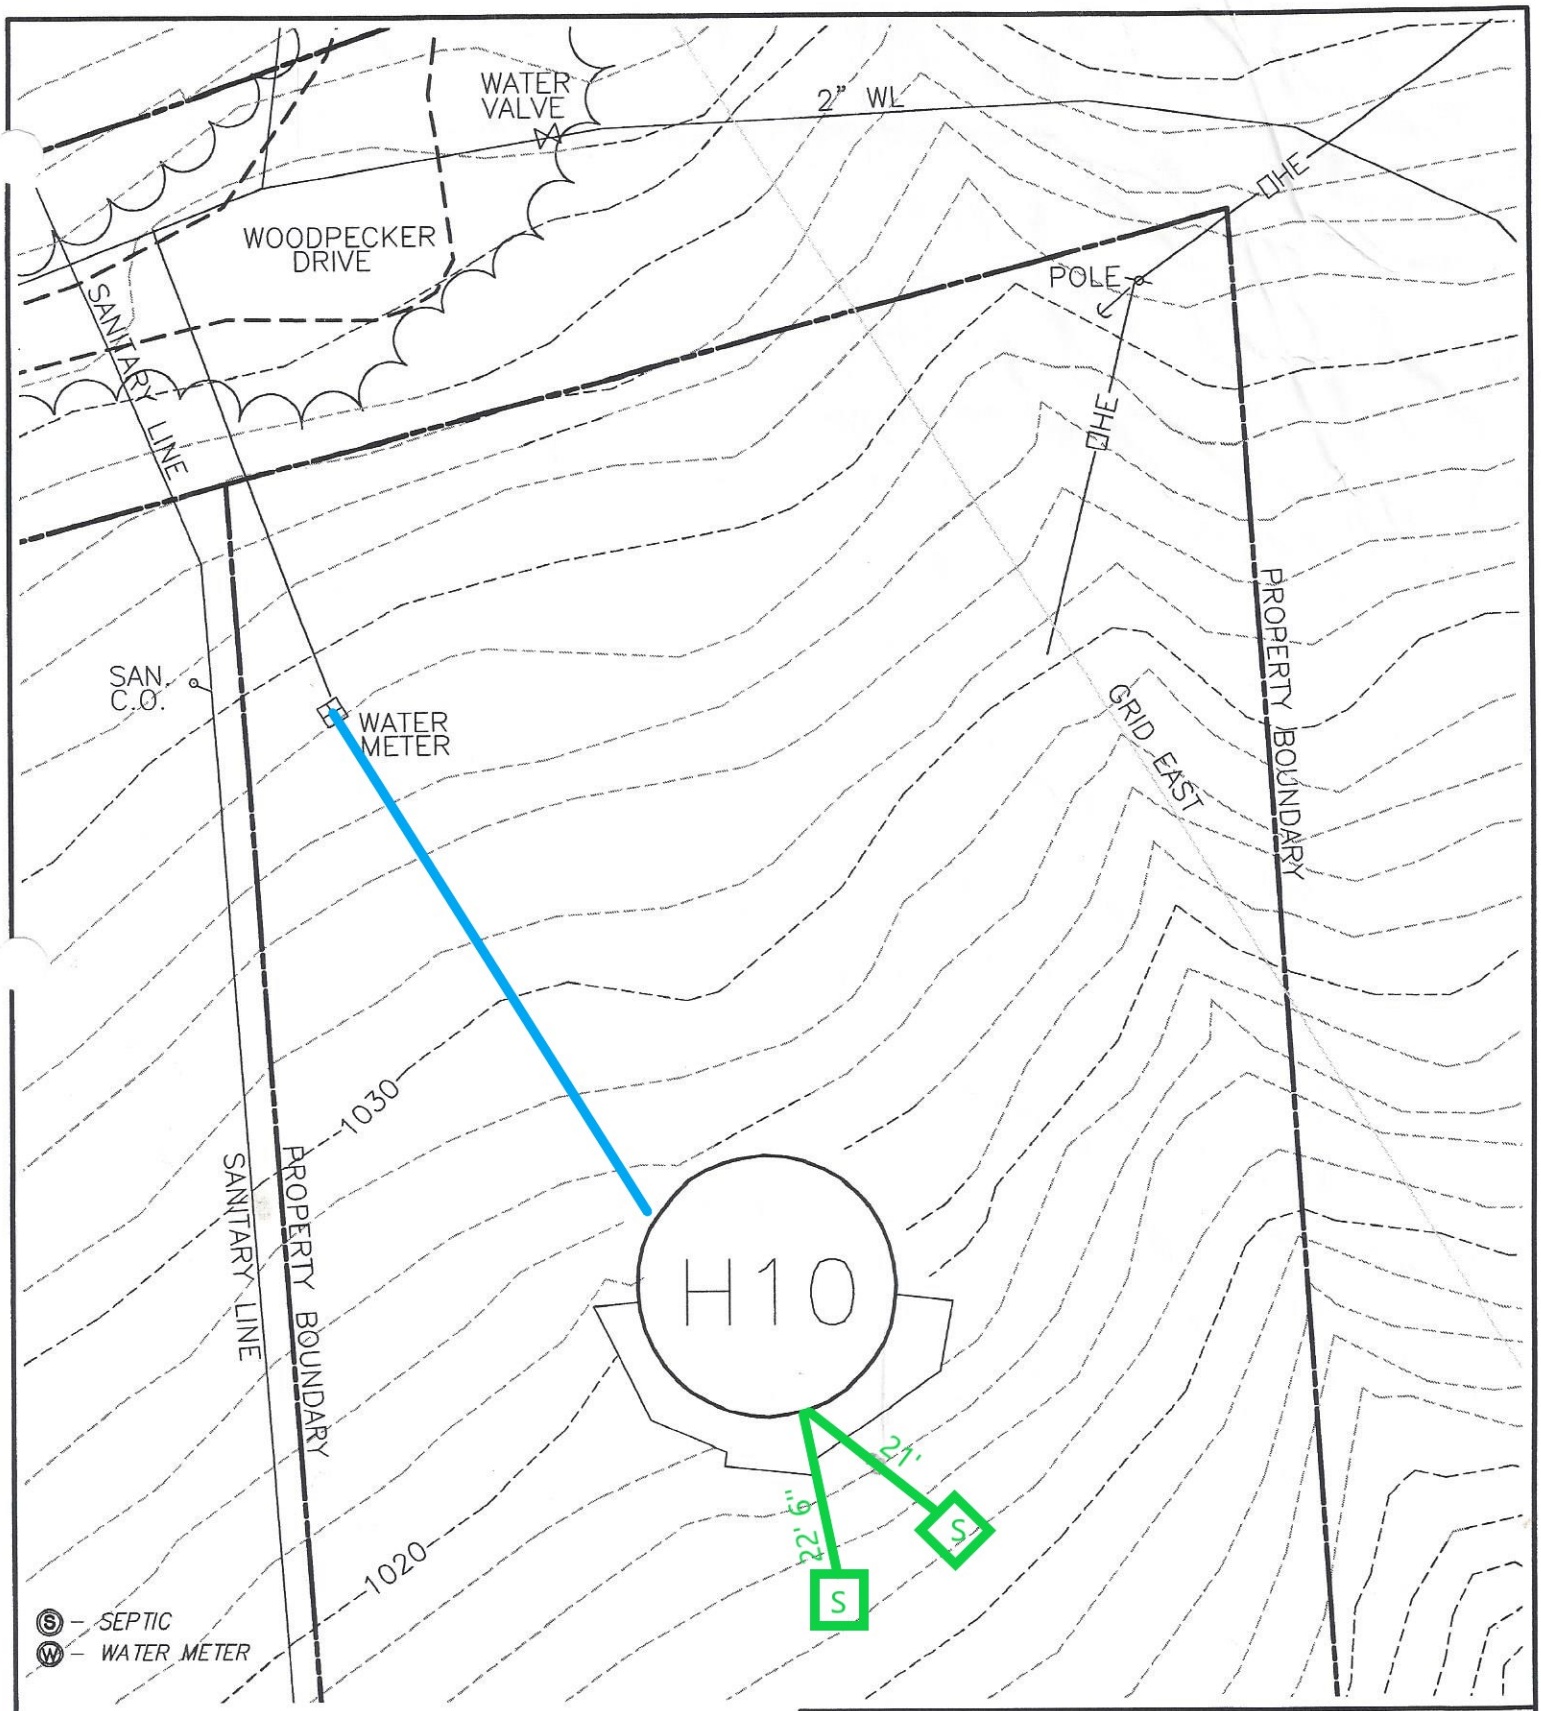

Septic tank
Septic tank
22ft. 6"
21ft.
Door in back
H-10
Front of House


Woodpecker



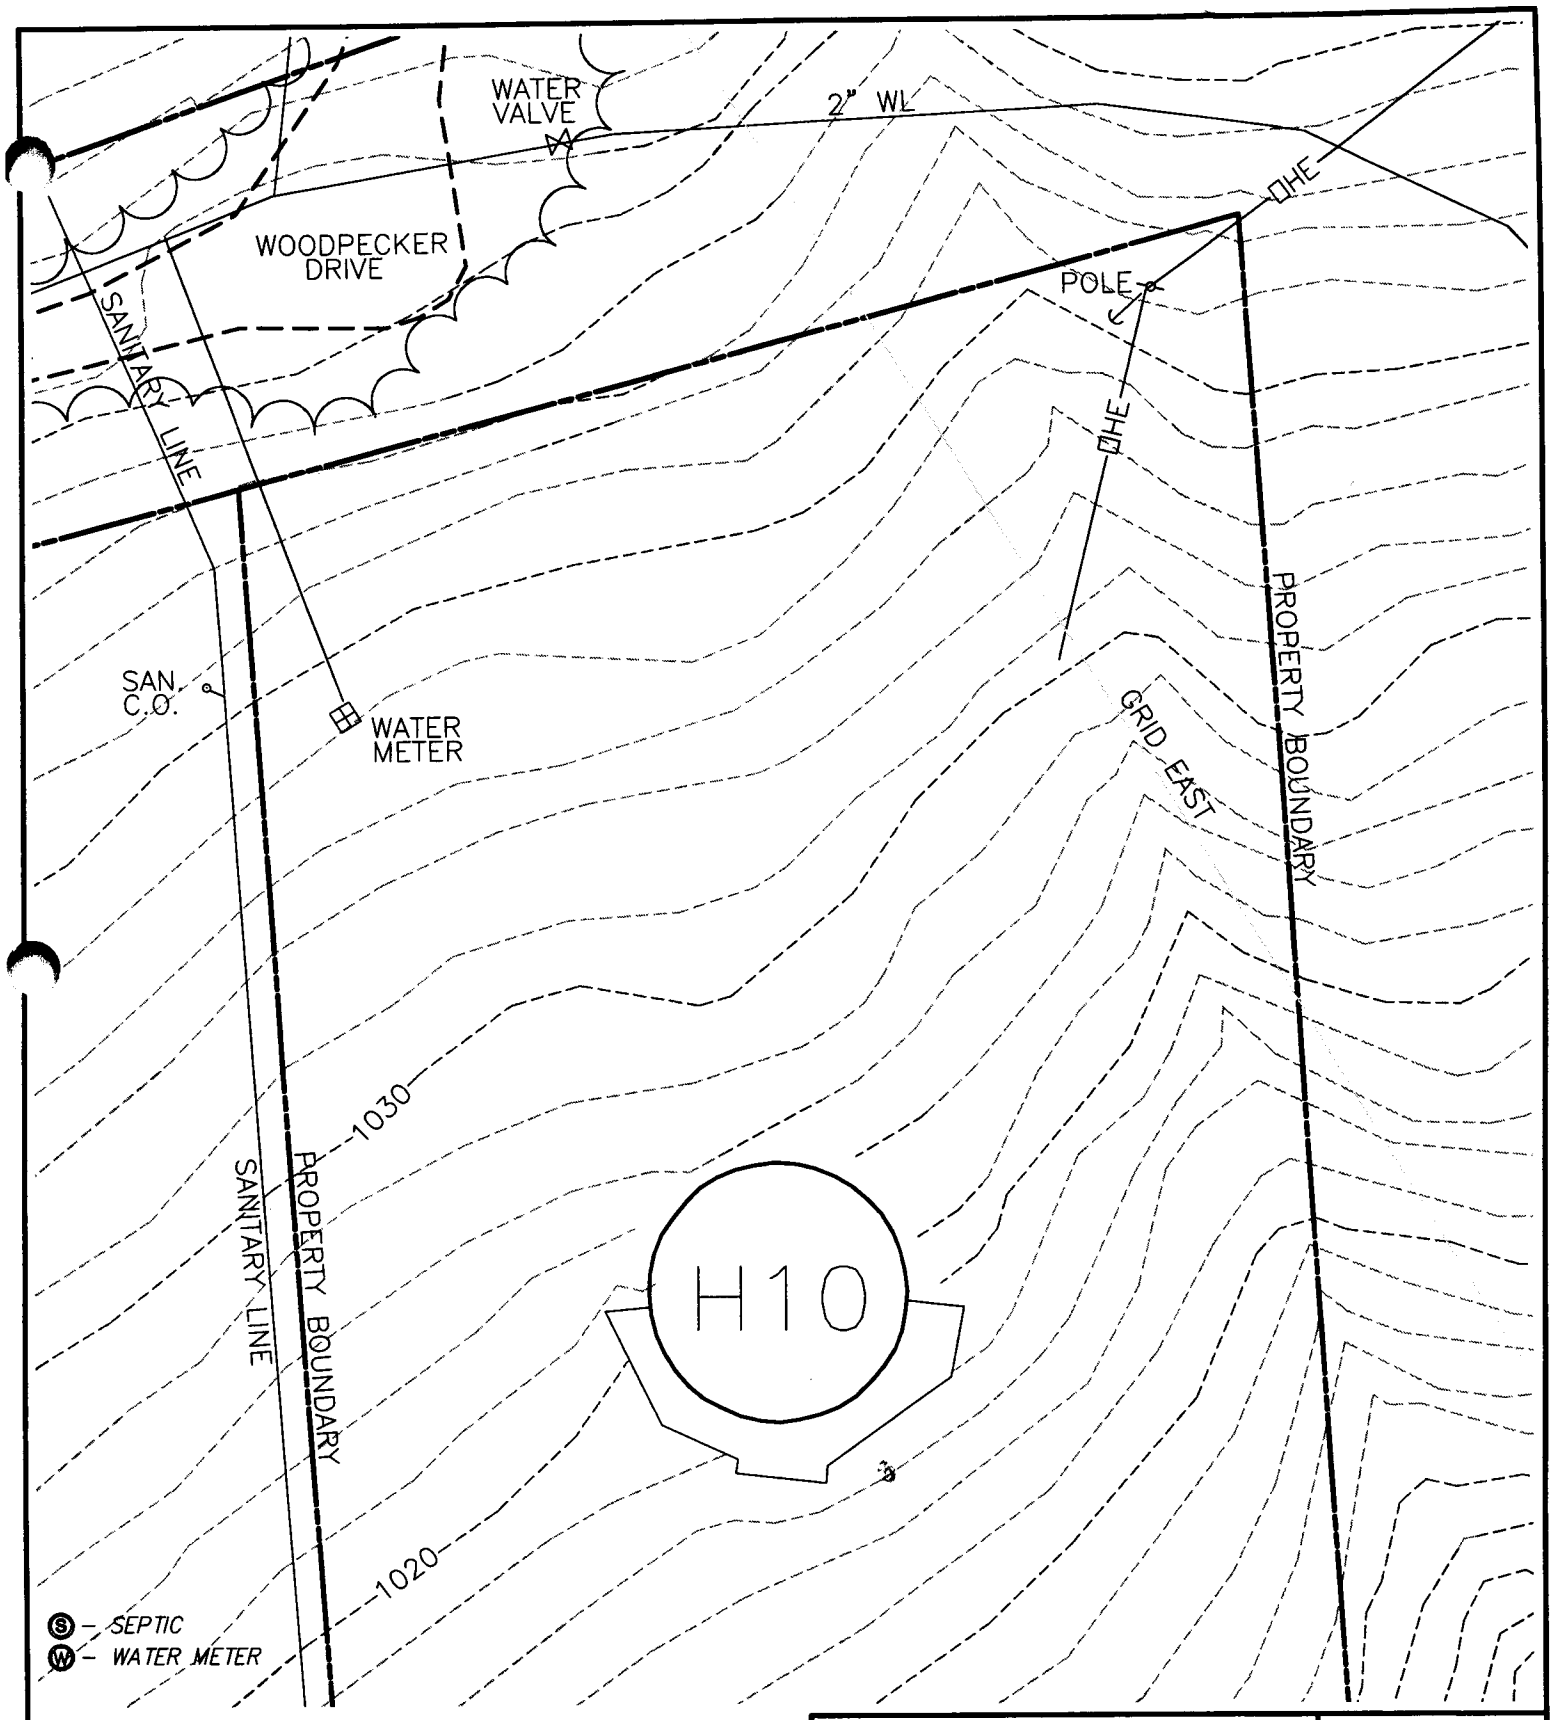


NOTE:
1. Property lines and utilities are shown in an approximated location.

208 WOODPECKER DRIVE SECTION H–LOT 10 UTILITY LOCATION MAP

SURVEY: PAS	C.I.: 2'
DRAWN BY: P–L	JOB NO.: 0902011
SCALE: SHOWN	DATE: 9/9/11
SHEET:	H10

C-32



30 0 30

Scale 1" = 30 ft

NOTE:
1. Property lines and utilities are shown in an approximated location.

208 WOODPECKER DRIVE SECTION H–LOT 10 UTILITY LOCATION MAP

SURVEY: PAS	C.I.: 2'
DRAWN BY: P–L	JOB NO.: 0902011
SCALE: SHOWN	DATE: 9/9/11
SHEET:	H10