
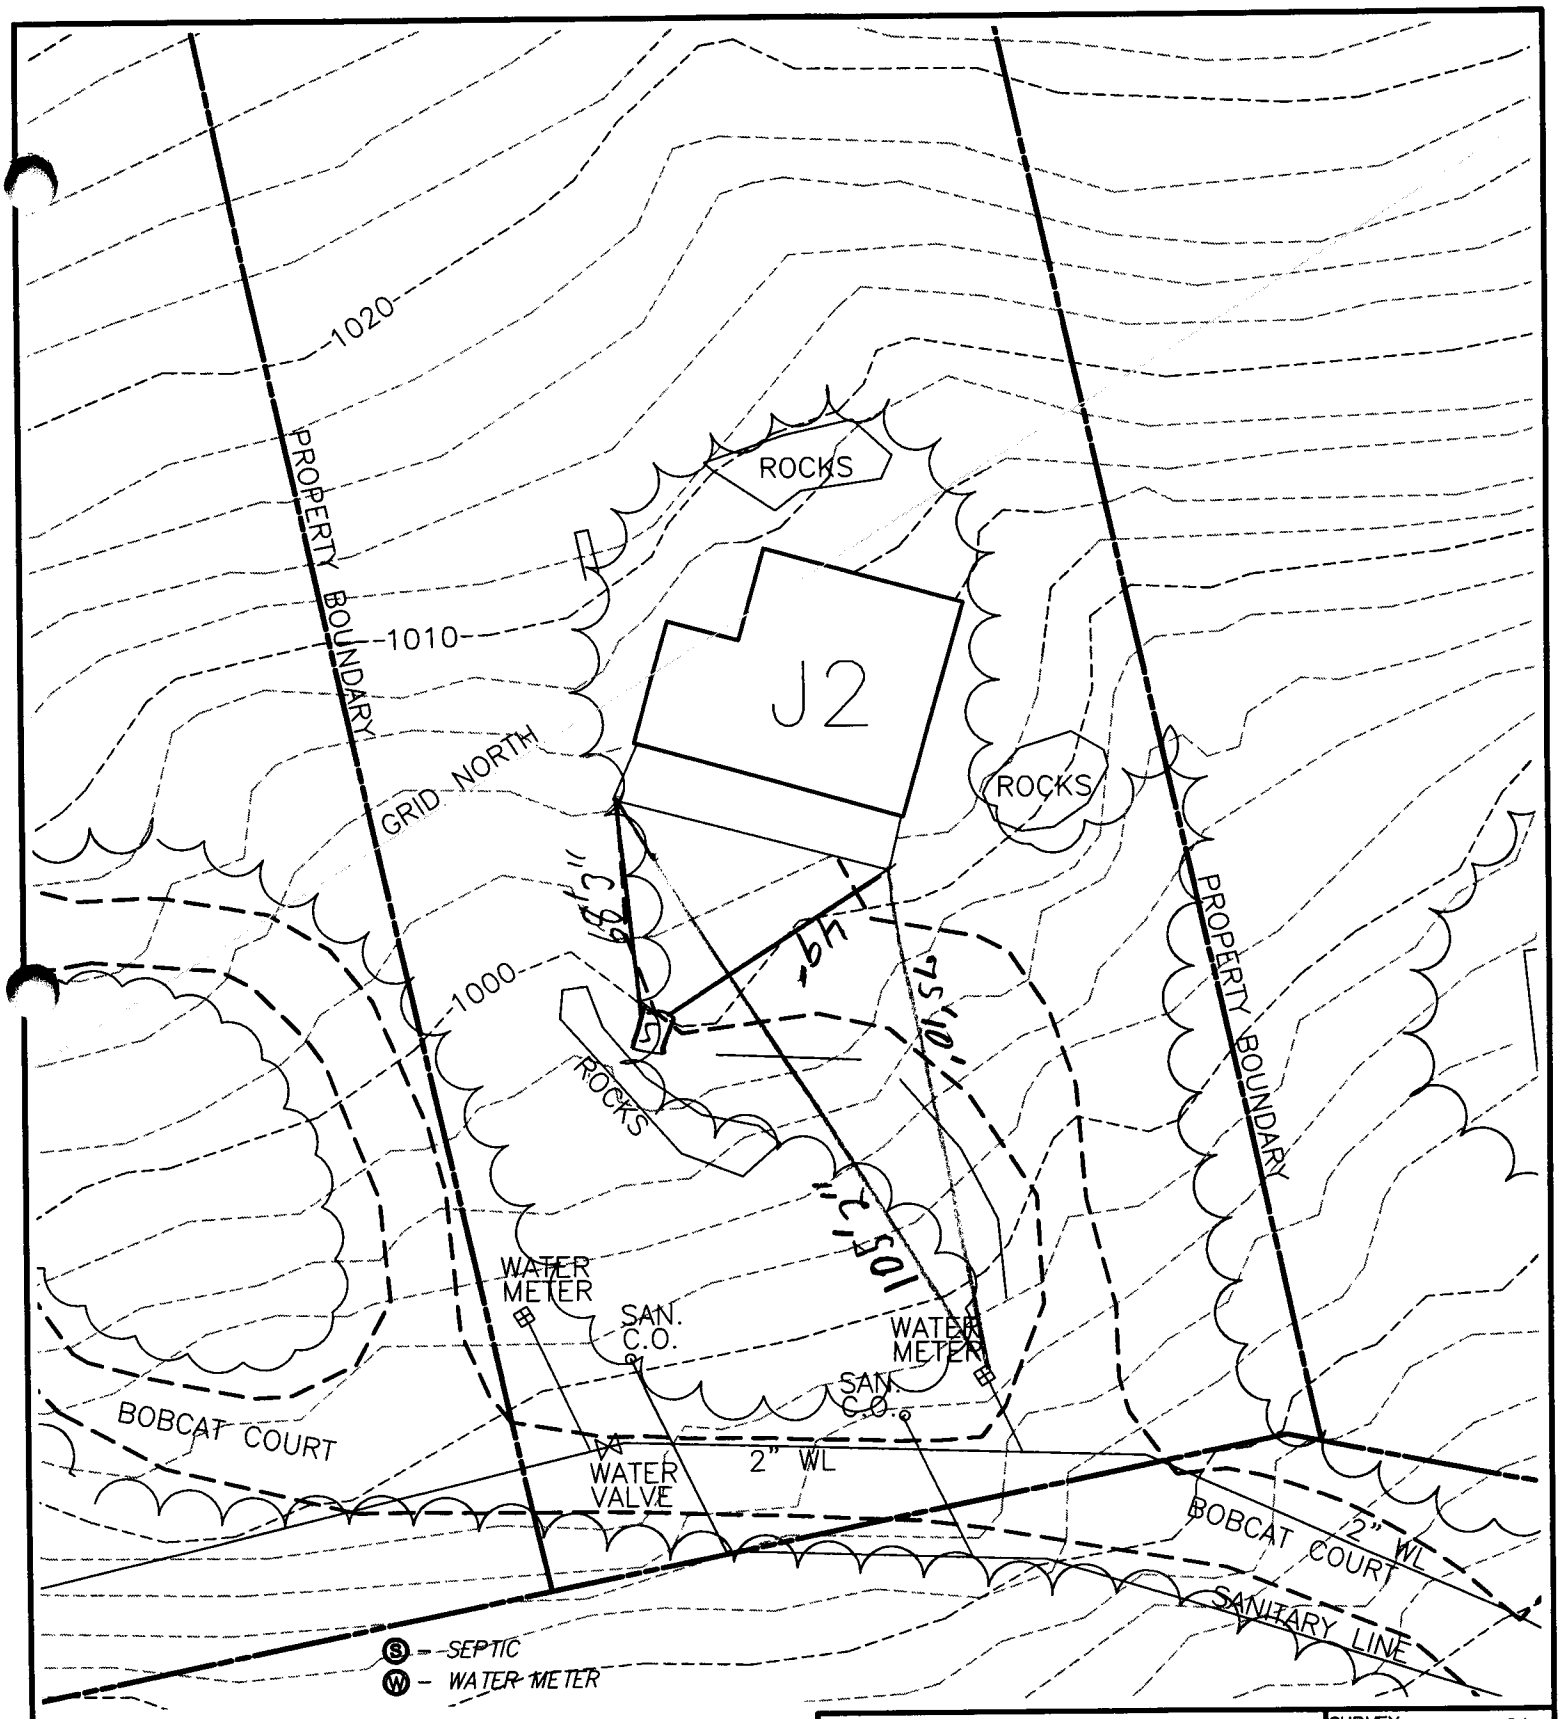


NOTE:
1. Property lines and utilities are shown in an approximated location.

34 BOBCAT COURT
SECTION J–LOT 2
UTILITY LOCATION MAP

SURVEY: PAS	C.I.: 2'
DRAWN BY: P–L	JOB NO.: 0902011
SCALE: SHOWN	DATE: 9/9/11
SHEET:	J2

3-3

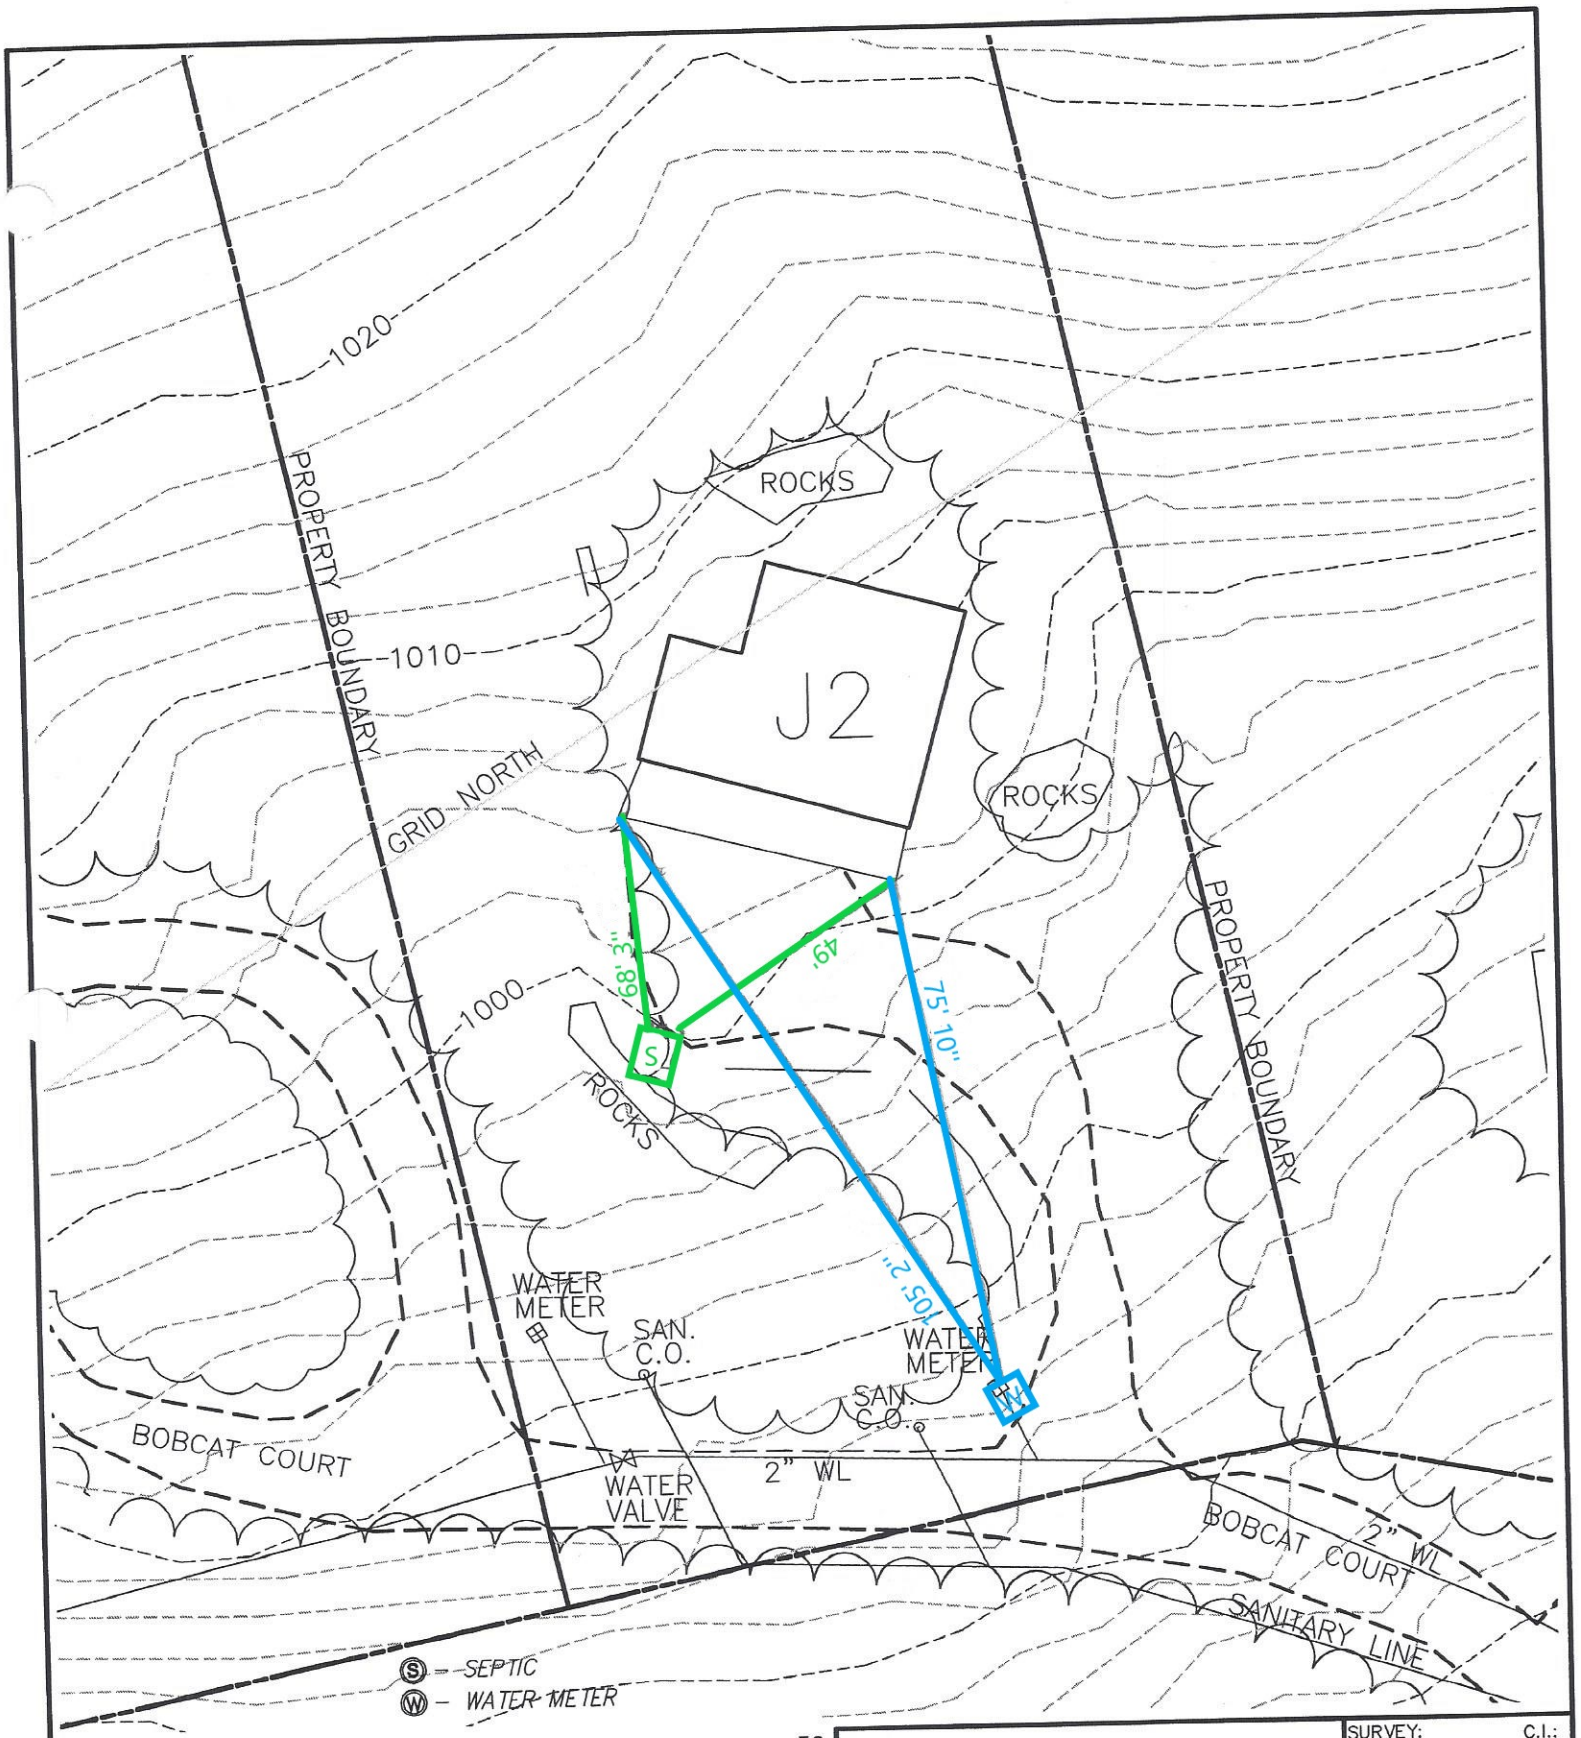

NOTE:
1. Property lines and utilities are shown in an approximated location.

34 BOBCAT COURT SECTION J–LOT 2 UTILITY LOCATION MAP

SURVEY: PAS	C.I.: 2'
DRAWN BY: P–L	JOB NO.: 0902011
SCALE: SHOWN	DATE: 9/9/11
SHEET:	J2

B-38