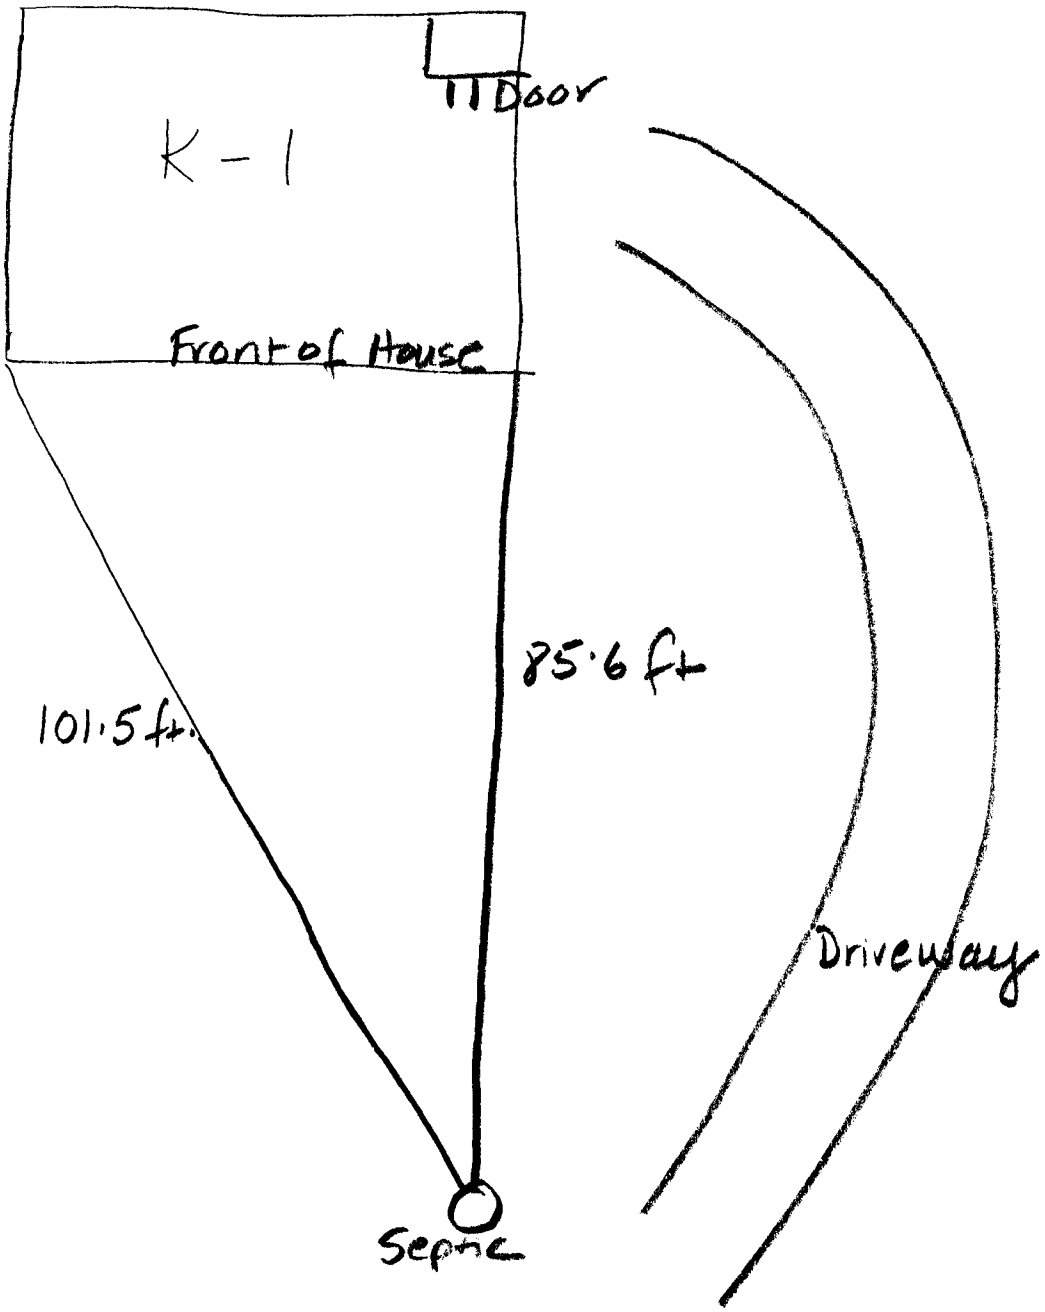
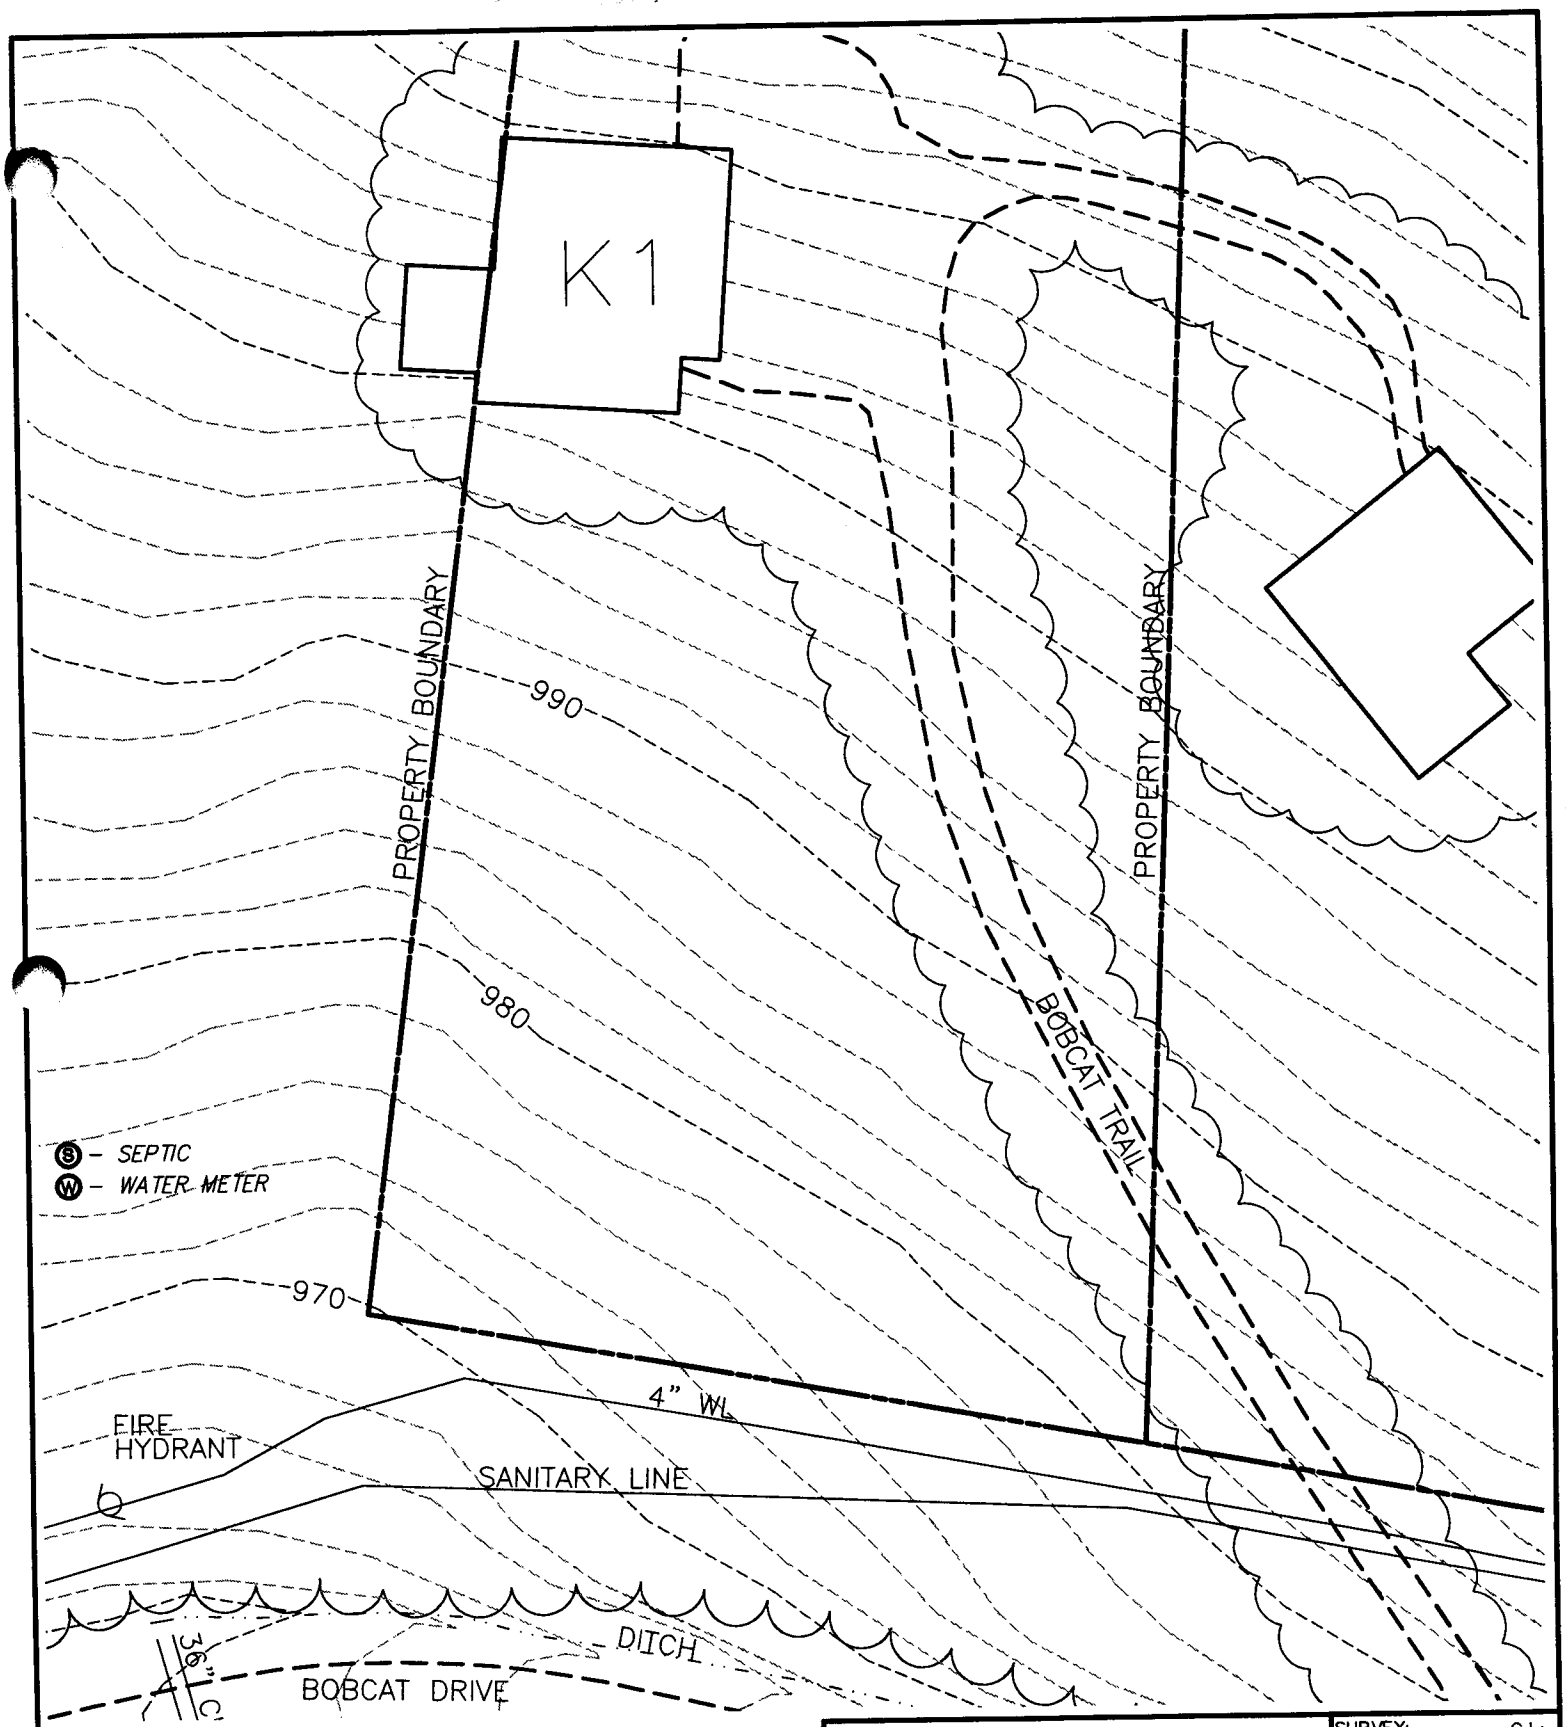

Door
K-1
Front of House
85.6 ft
101.5 ft.
Driveway
Septic

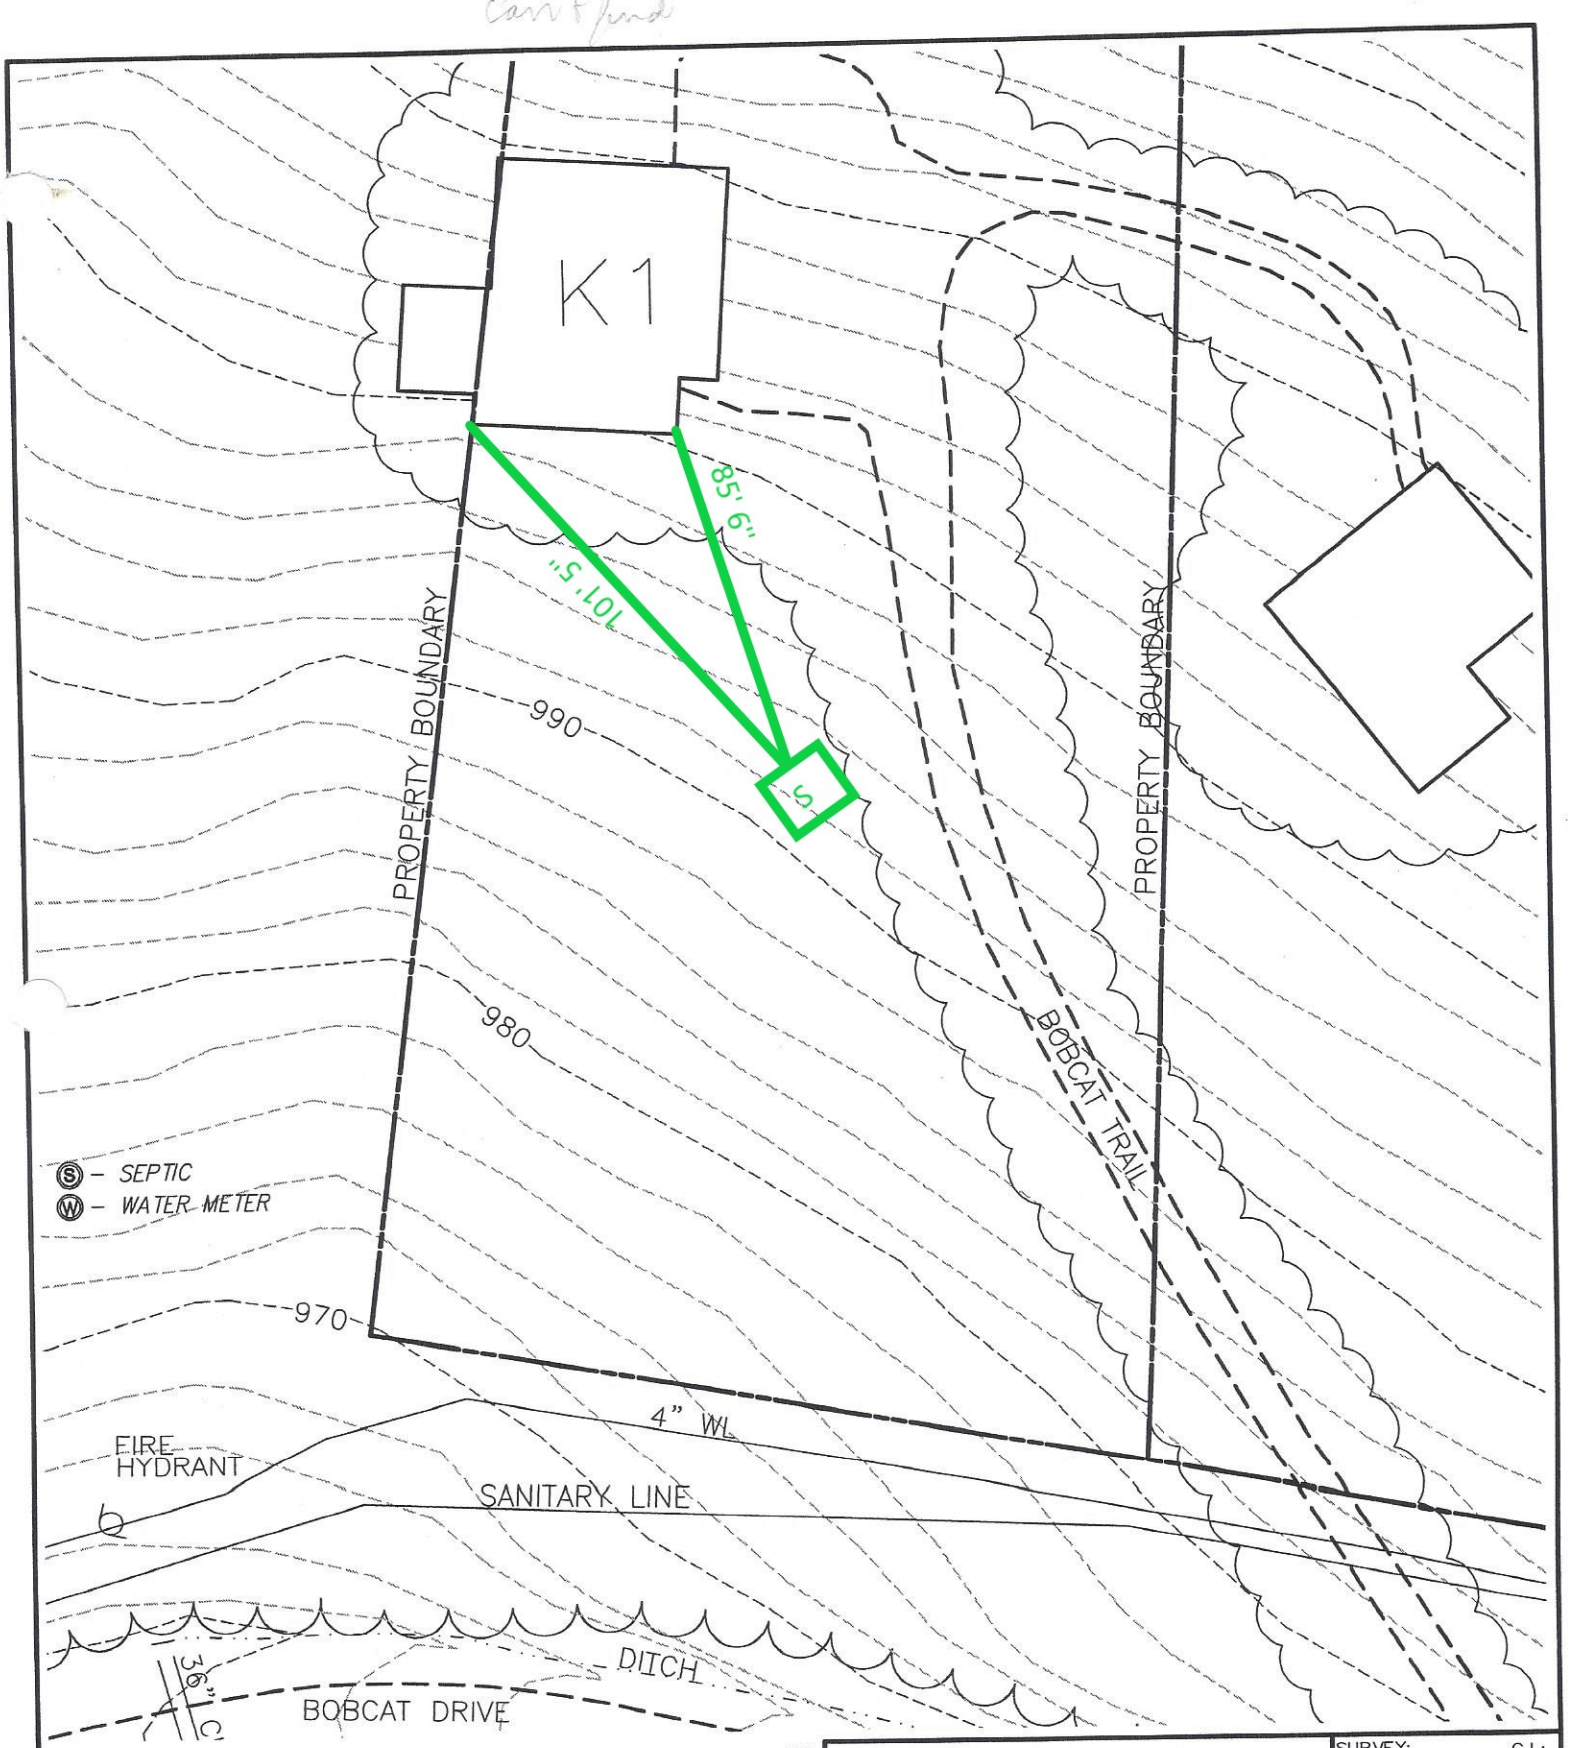


NOTE:
1. Property lines and utilities are shown in an approximated location.

55 BOBCAT TRAIL
SECTION K–LOT 1
UTILITY LOCATION MAP

SURVEY: PAS	C.I.: 2'
DRAWN BY: P–L	JOB NO.: 0902011
SCALE: SHOWN	DATE: 9/9/11
SHEET:	K1

C-1



NOTE:
1. Property lines and utilities are shown in an approximated location.

55 BOBCAT TRAIL
SECTION K–LOT 1
UTILITY LOCATION MAP

SURVEY: PAS	C.I.: 2'
DRAWN BY: P–L	JOB NO.: 0902011
SCALE: SHOWN	DATE: 9/9/11
SHEET:	K1

C-1