


Q-4
1999

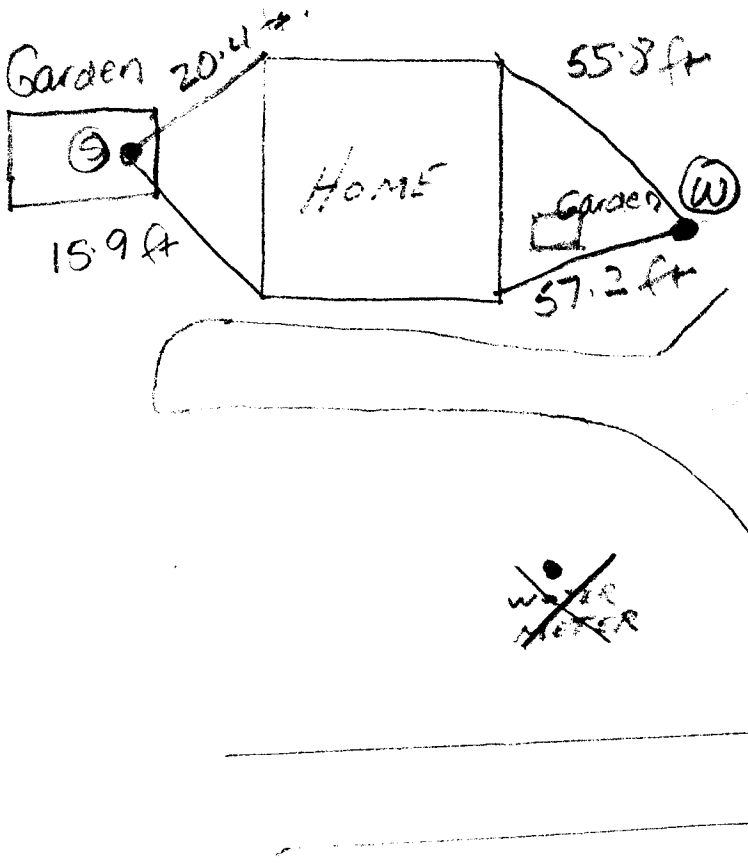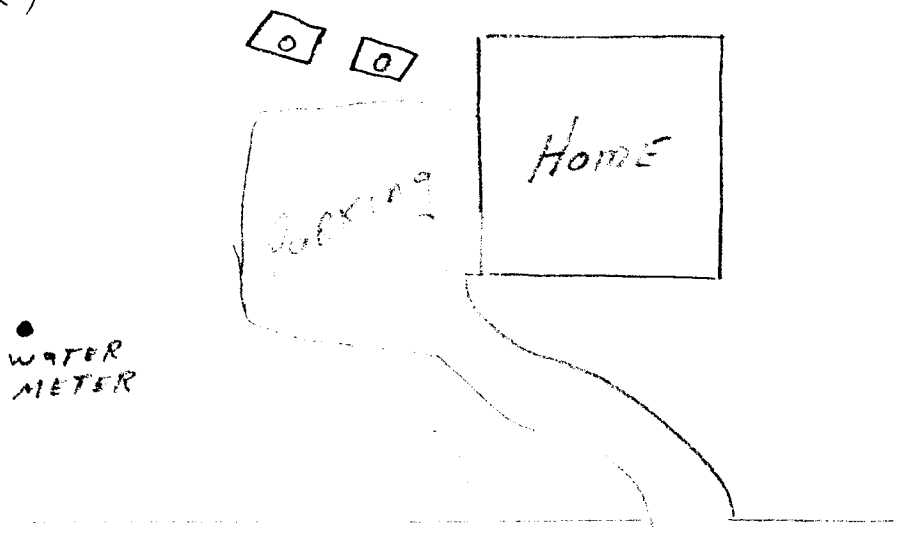


Q-5
1999

SEPTIC Lids
at Ground level
(2)

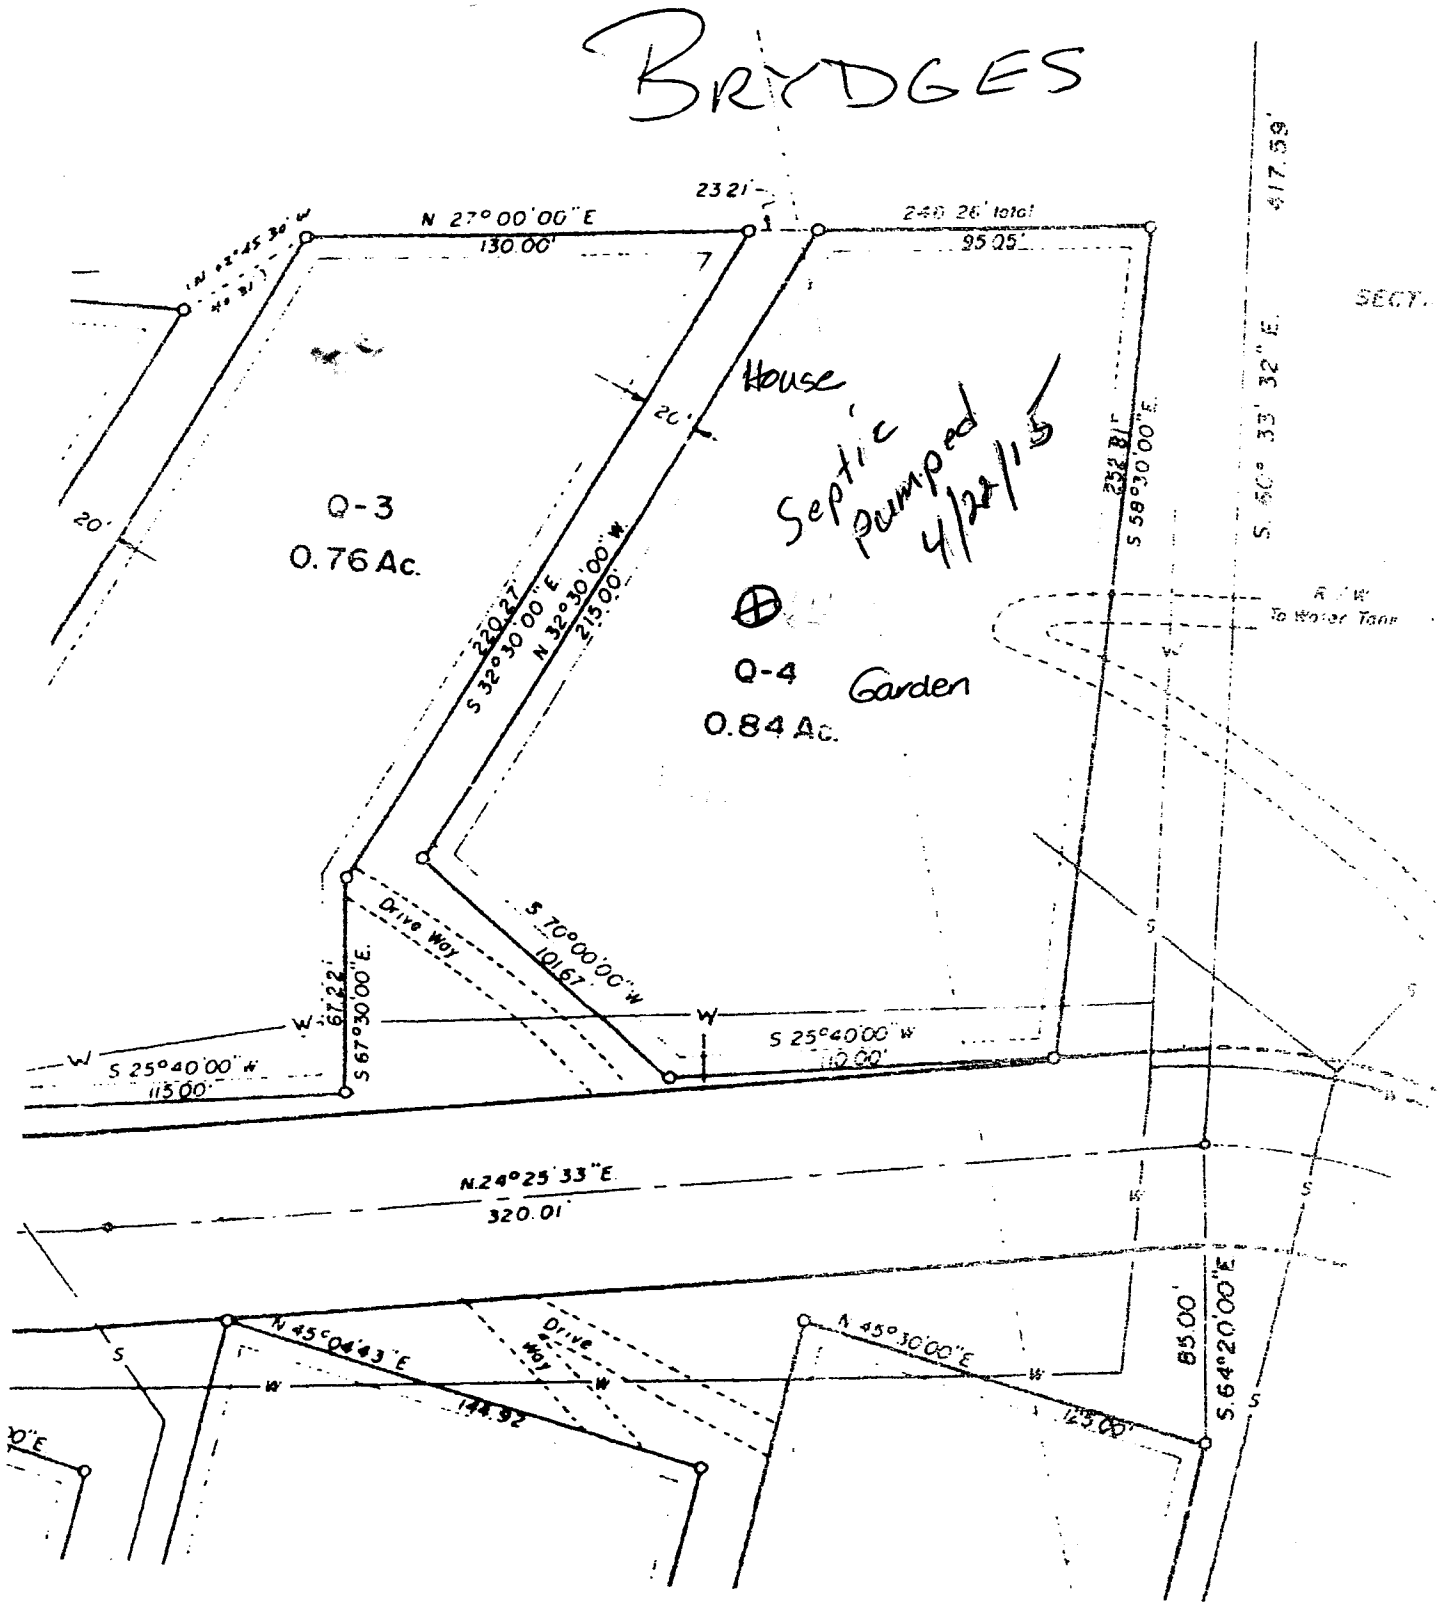


BRYDGES
N 27°00'00" E
130.00'
232.1'
240.26' total
95.05'
417.59'
SECT.
S. 60° 33' 32" E.
House
Septic pumped 4/22/15
20'
Q-3
0.76 Ac.
Q-4
0.84 Ac.
Garden
S 32°30'00" E
220.27'
N 32°30'00" W
215.00'
S 58°30'00" E.
232.81'
To Water Tank
Drive Way
S 70°00'00" W
101.67'
S 67°30'00" E.
67.22'
S 25°40'00" W
113.00'
S 25°40'00" W
42.00'
N.24°25'33" E
320.01'
N 45°04'43" E
144.92'
N 45°30'00" E
125.00'
85.00'
S.64°20'00" E

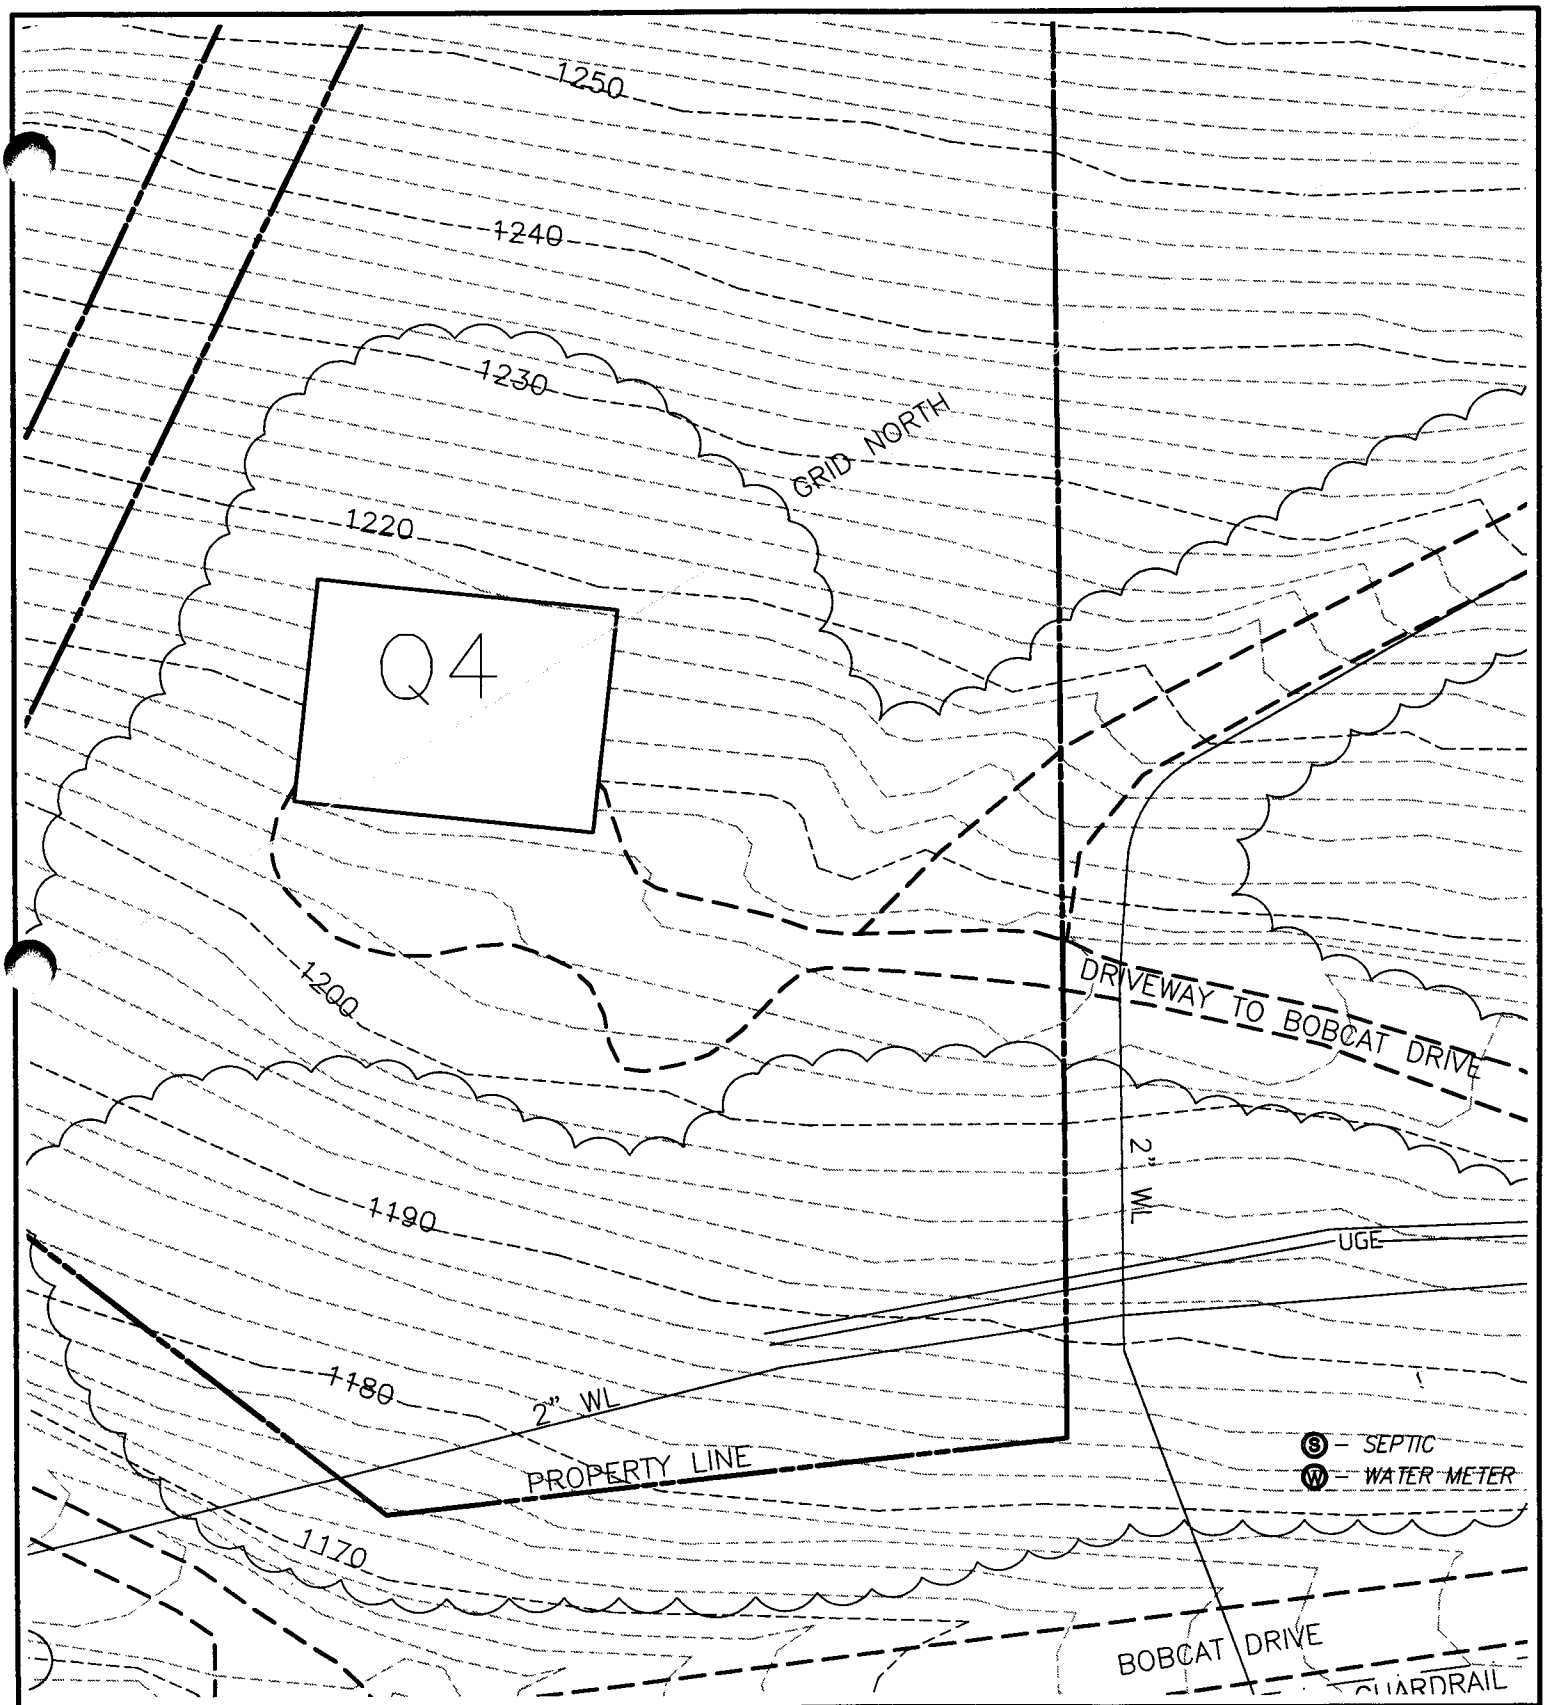

30 0 30

Scale 1" = 30 ft

NOTE:
1. Property lines and utilities are shown in an approximated location.

537 BOBCAT DRIVE
SECTION Q–LOT 4
UTILITY LOCATION MAP

SURVEY: PAS	C.I.: 2'
DRAWN BY: P–L	JOB NO.: 0902011
SCALE: SHOWN	DATE: 9/9/11
SHEET:	Q4