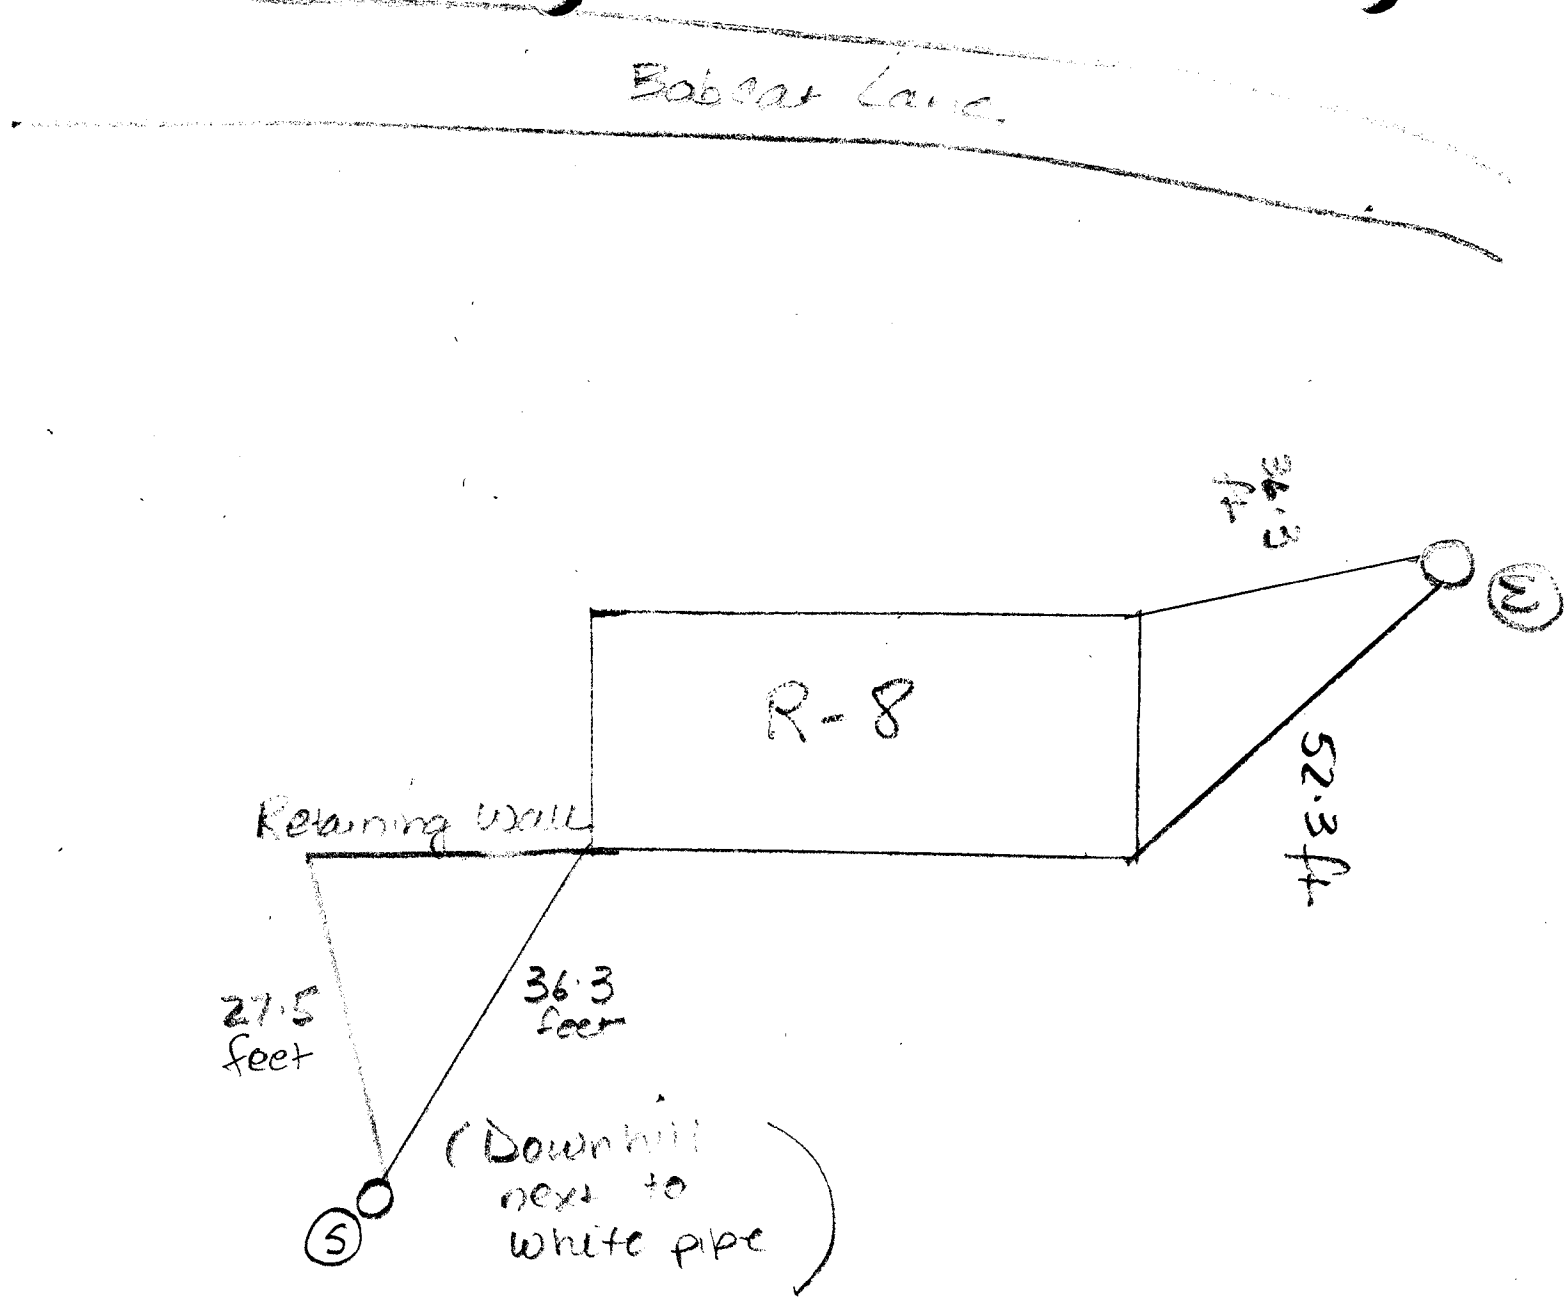
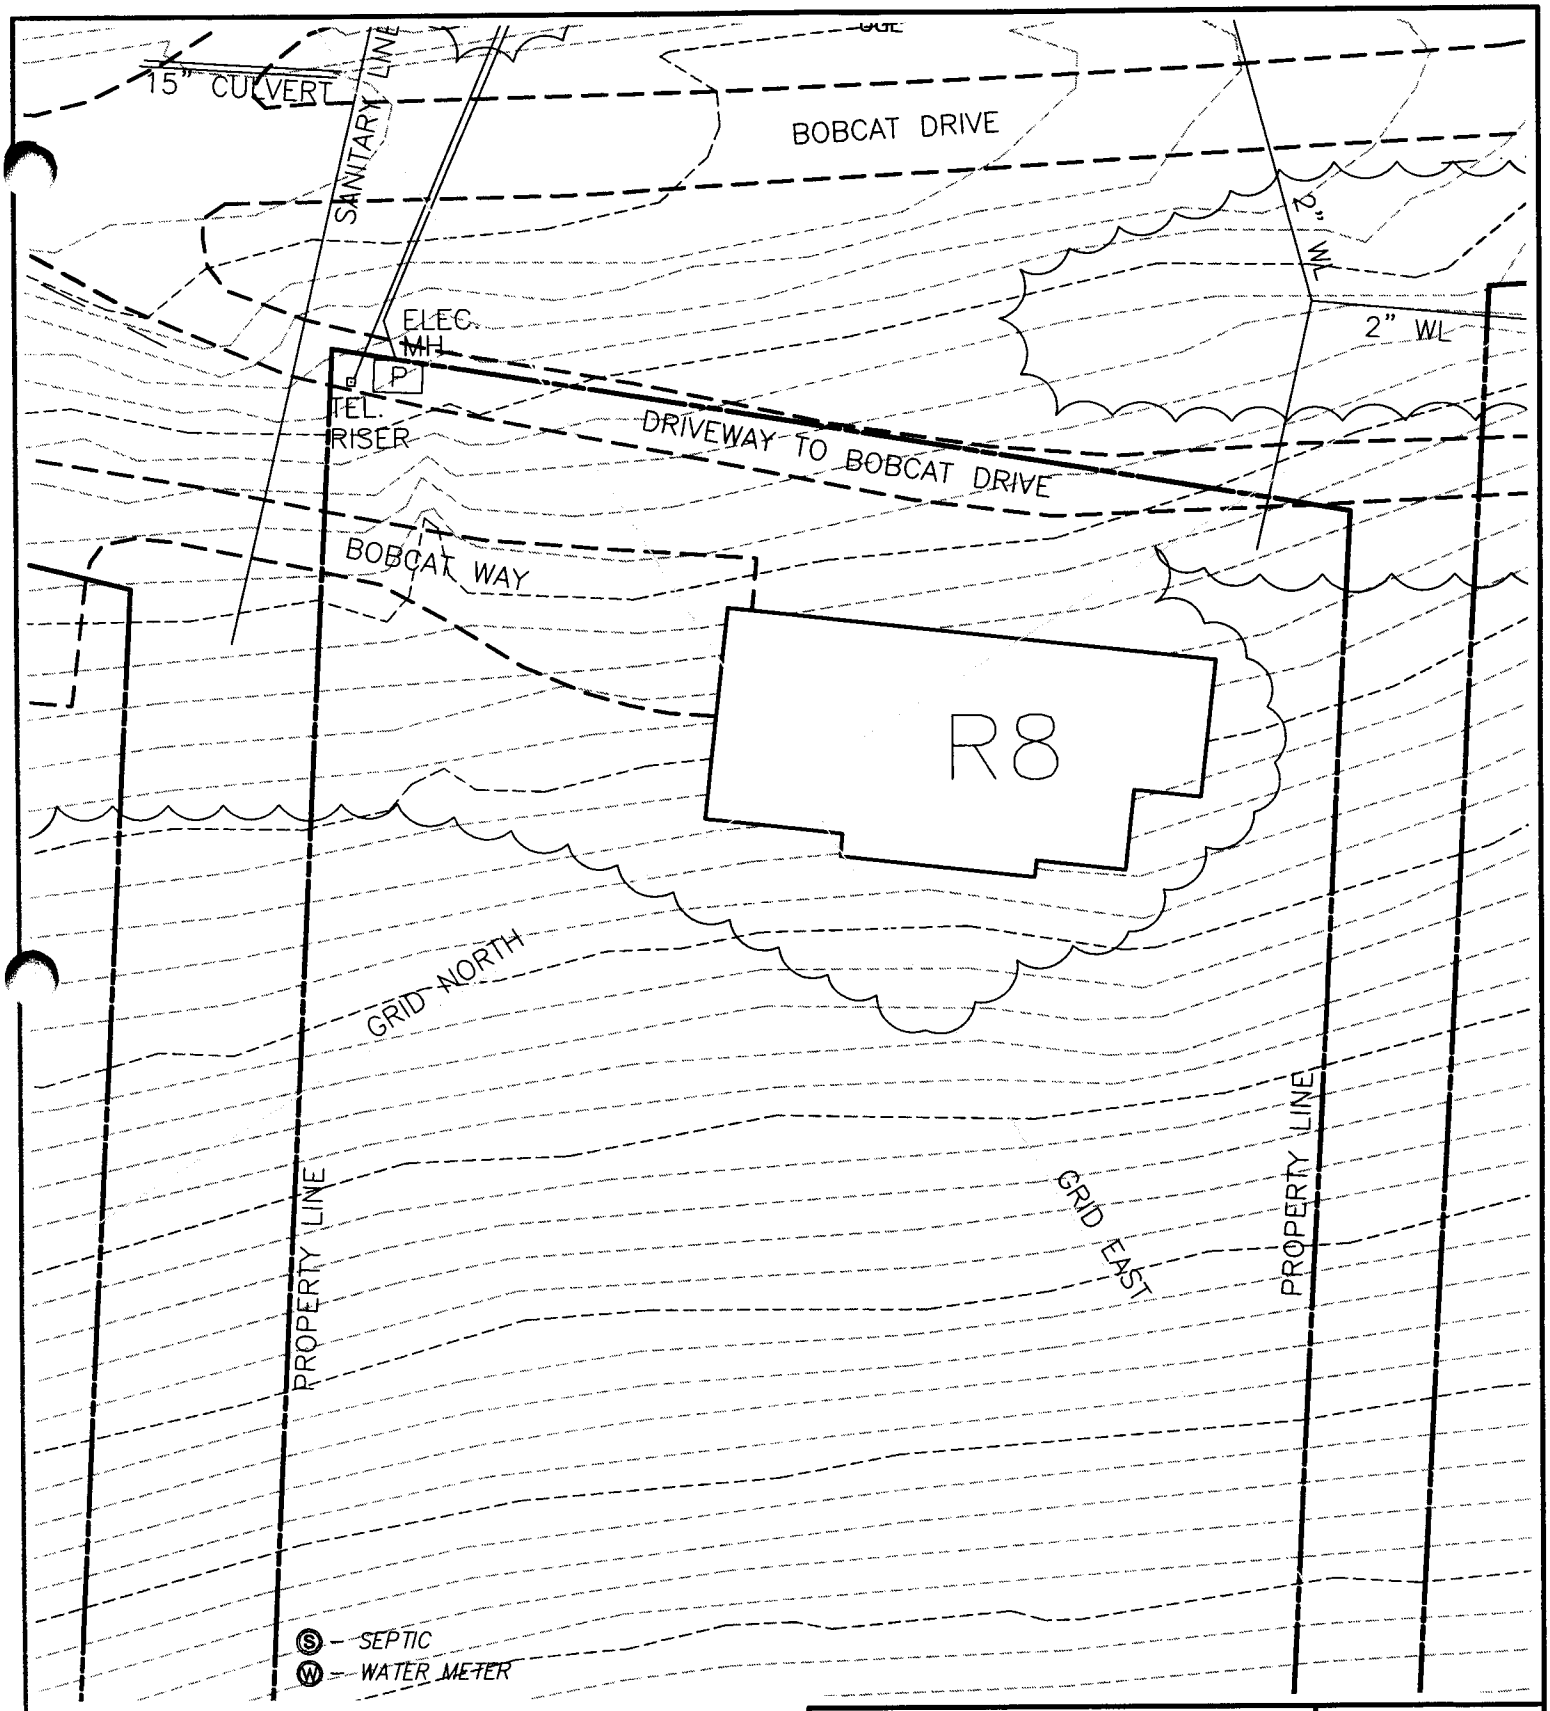

Bobcat Lane
R-8
Retaining Wall
27.5 feet
36.3 feet
52.3 ft.
(5)
(Downhill next to white pipe)



30 0 30

Scale 1" = 30 ft

NOTE:
1. Property lines and utilities are shown in an approximated location.

50 BOBCAT WAY
SECTION R–LOT 8
UTILITY LOCATION MAP

SURVEY: PAS	C.I.: 2'
DRAWN BY: P–L	JOB NO.: 0902011
SCALE: SHOWN	DATE: 9/9/11
SHEET:	R8

B-80