

S-1
199

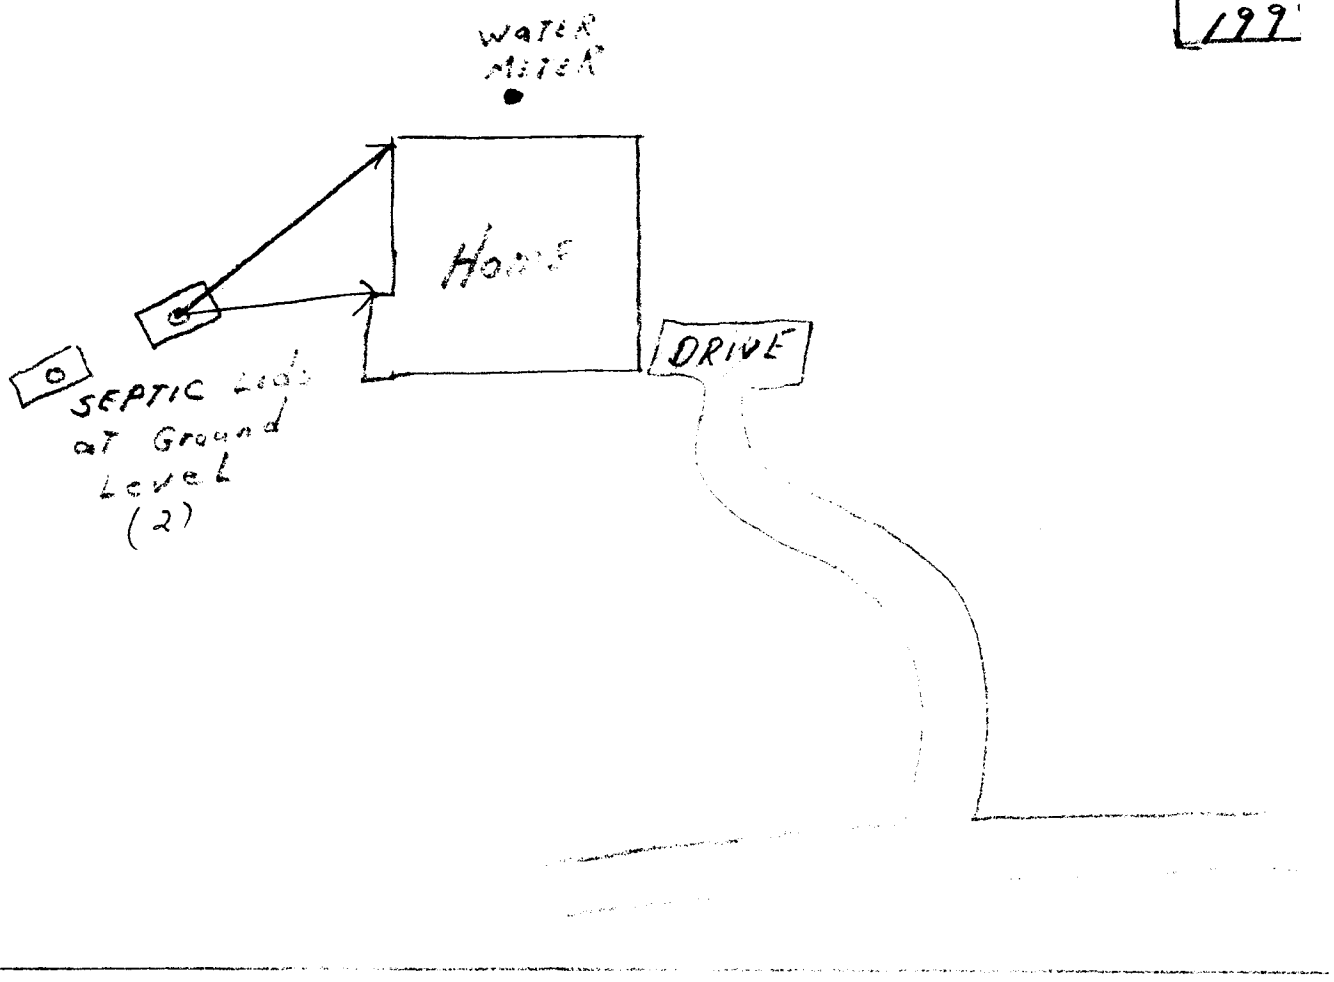

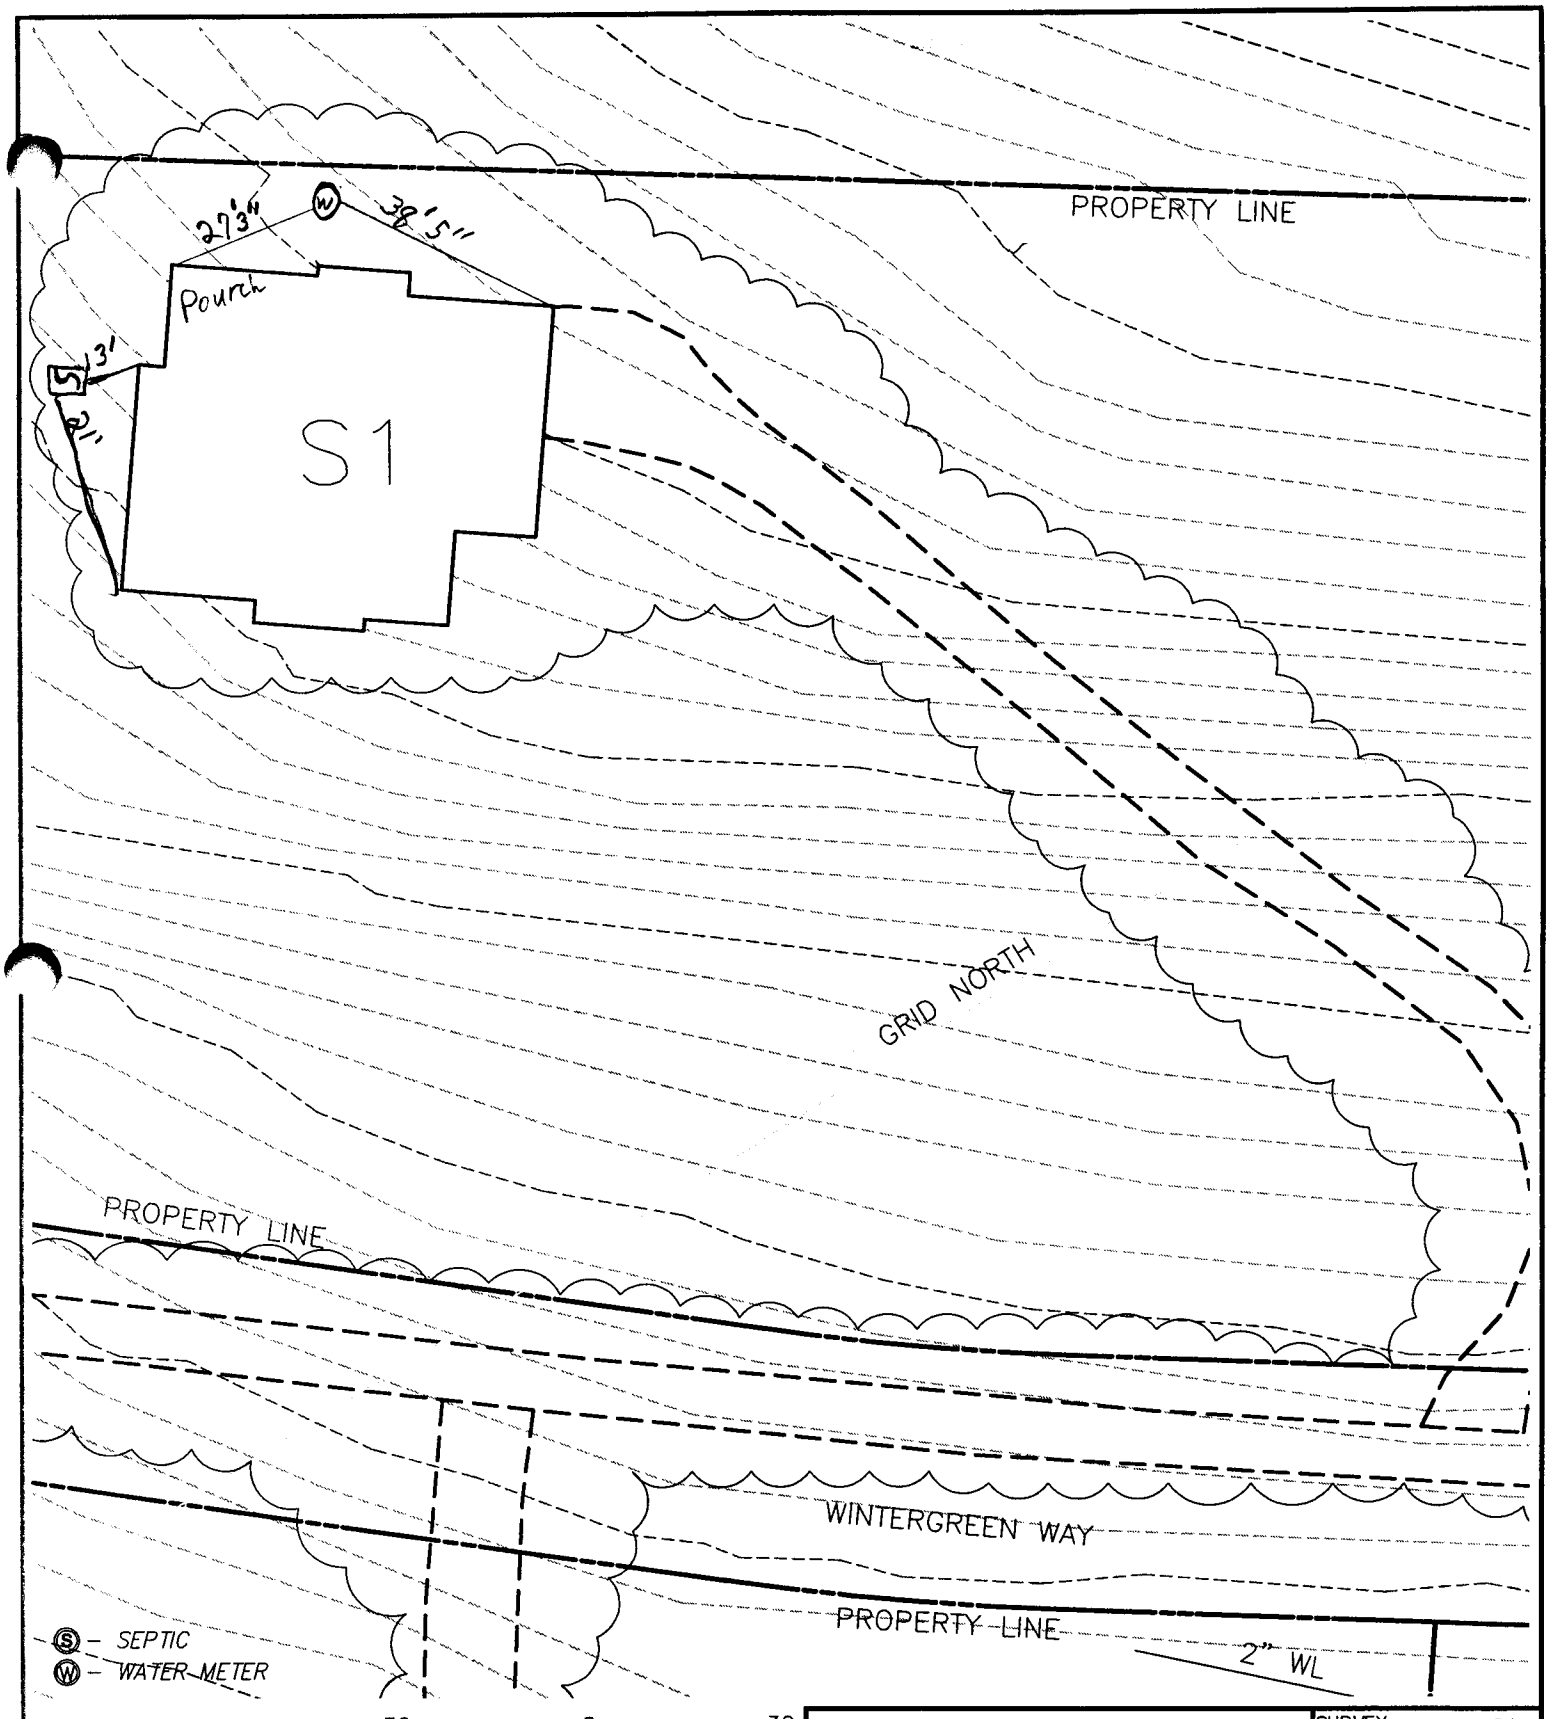

NOTE:
1. Property lines and utilities are shown in an approximated location.

327 WINTERGREEN WAY
SECTION S–LOT 1
UTILITY LOCATION MAP

SURVEY: PAS	C.I.: 2'
DRAWN BY: P–L	JOB NO.: 0902011
SCALE: SHOWN	DATE: 9/9/11
SHEET:	S1

3-SC