


S-2
1999

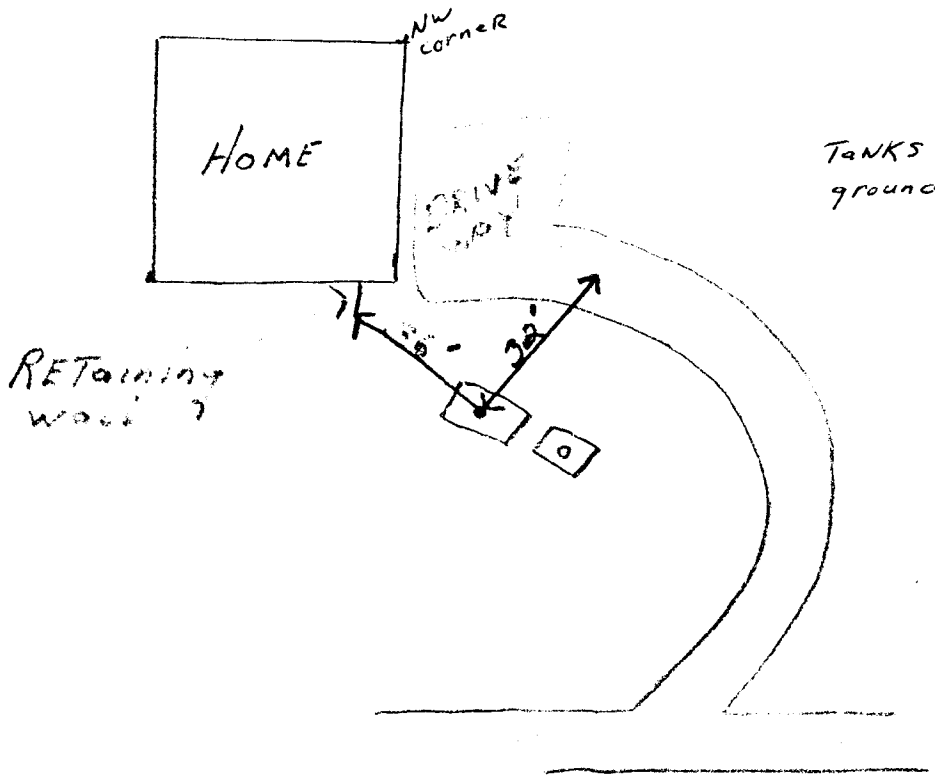

S-3
1999

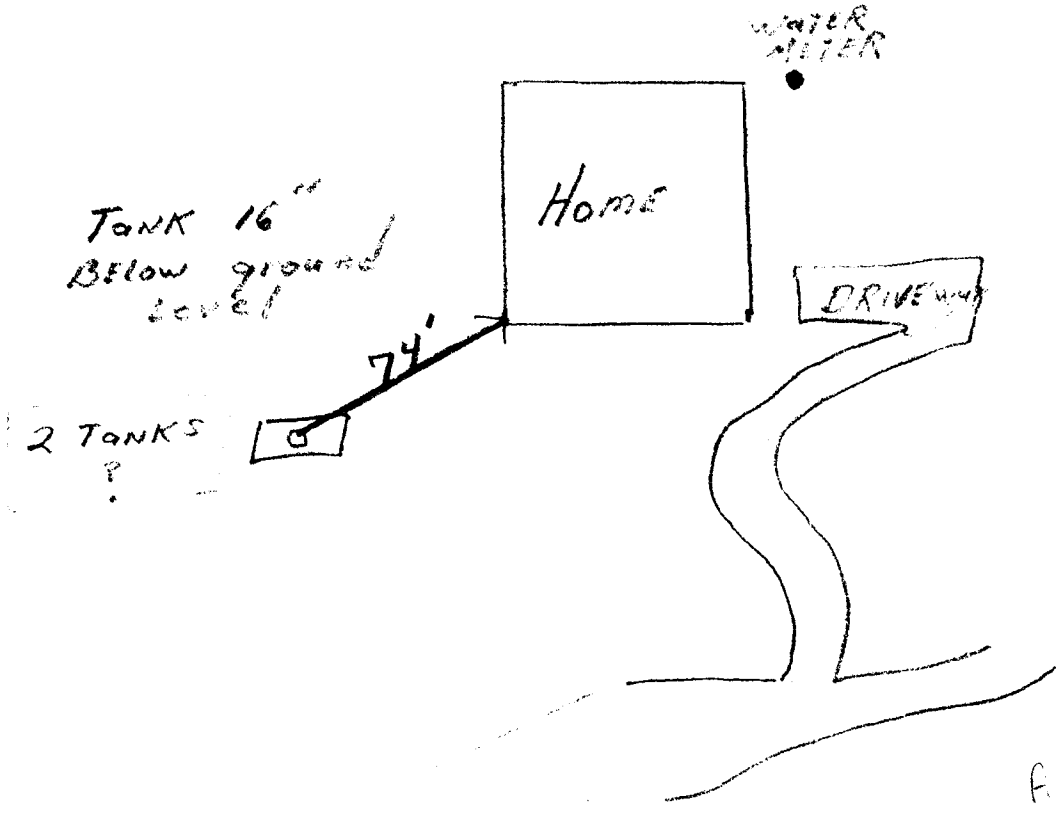

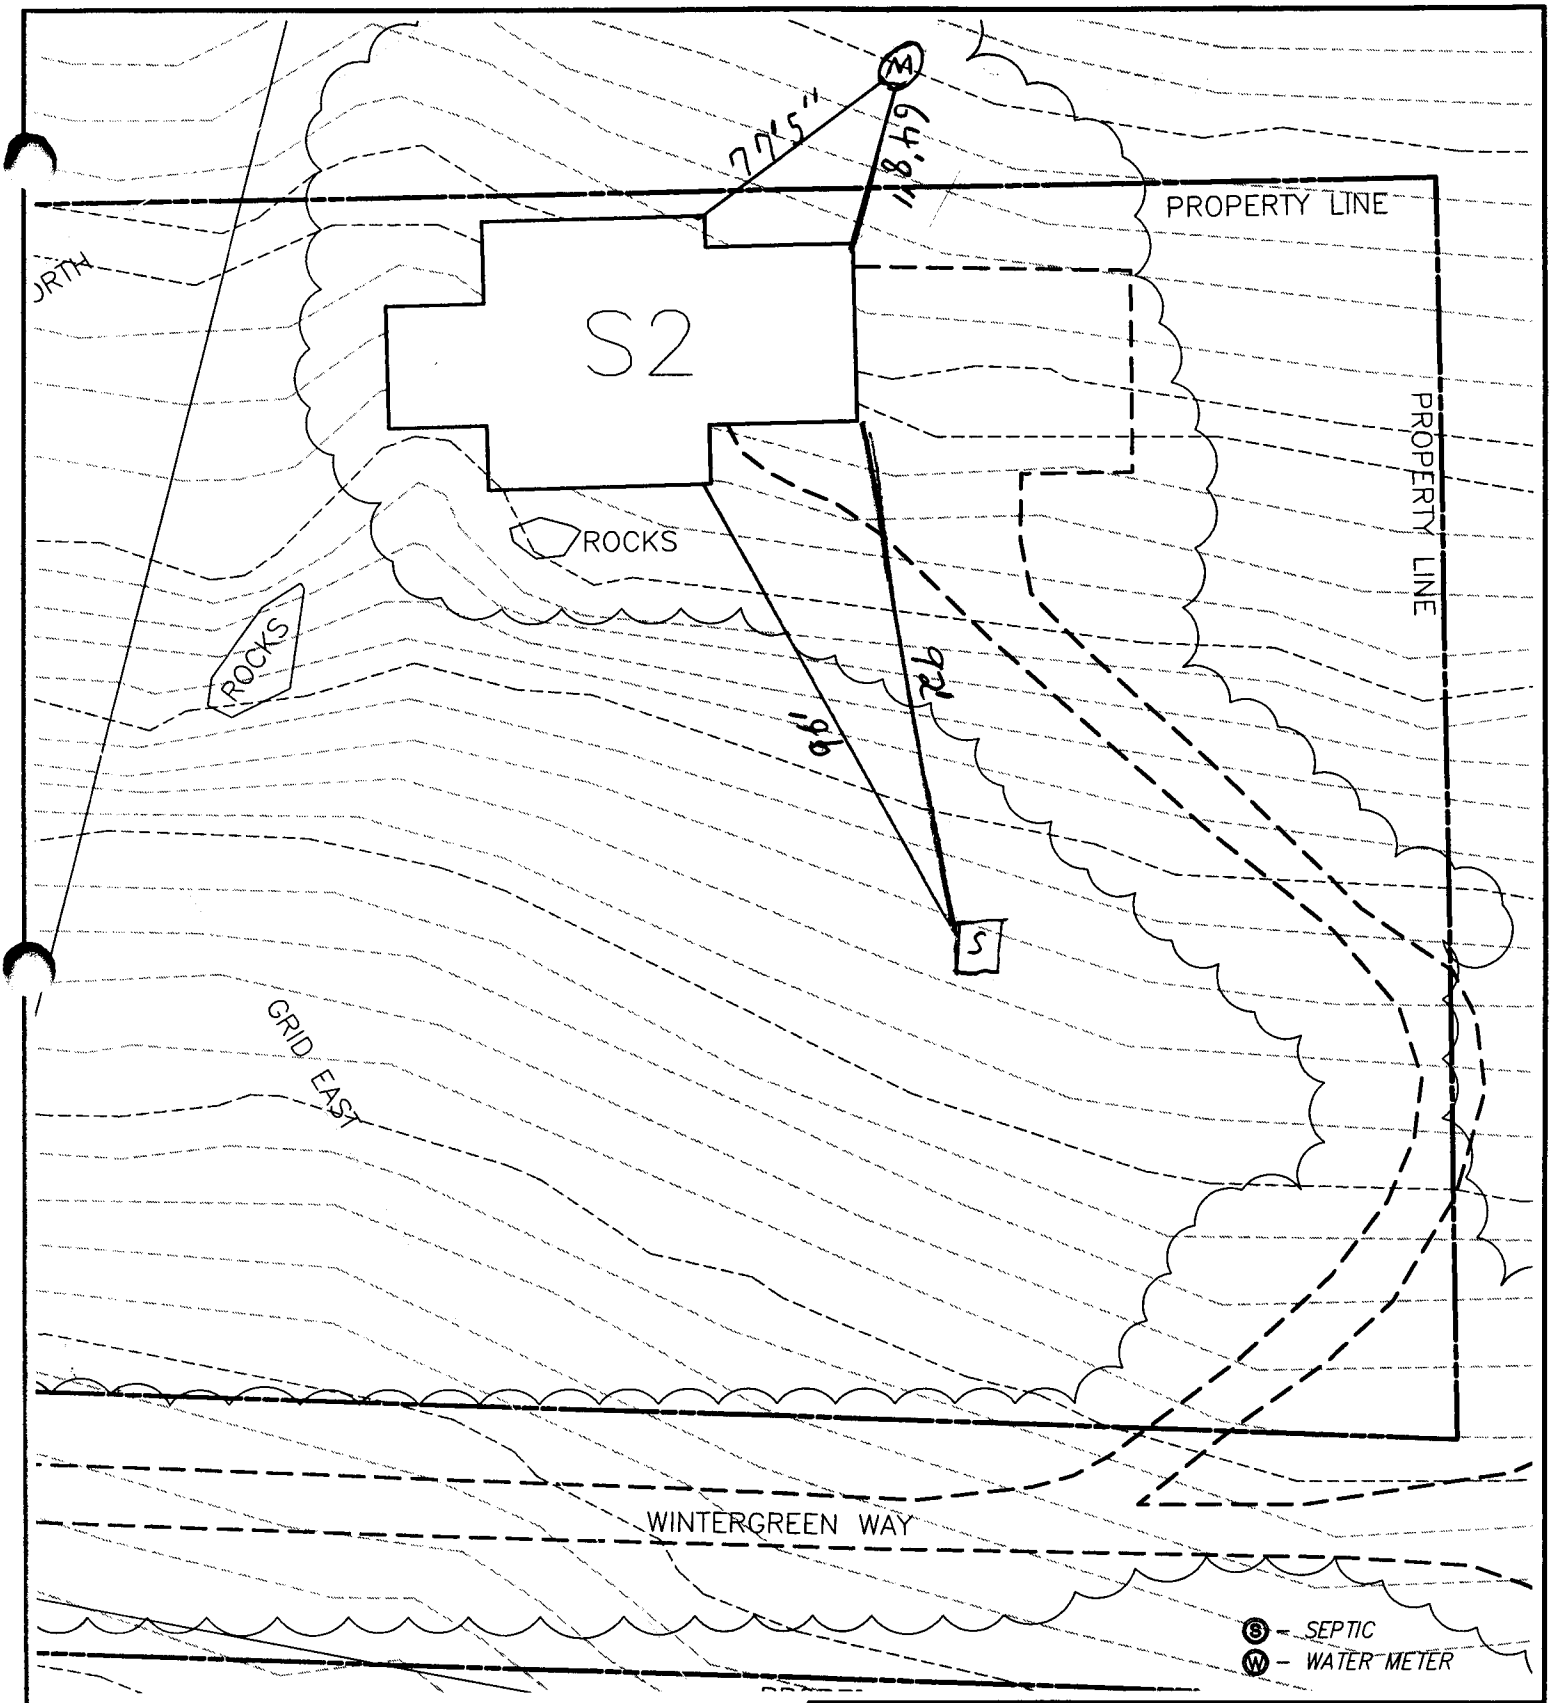

30 0 30

Scale 1" = 30 ft

NOTE:
1. Property lines and utilities are shown in an approximated location.

379 WINTERGREEN WAY
SECTION S–LOT 2
UTILITY LOCATION MAP

SURVEY: PAS	C.I.: 2'
DRAWN BY: P–L	JOB NO.: 0902011
SCALE: SHOWN	DATE: 9/9/11
SHEET:	S2

C-45