


S-2
1999

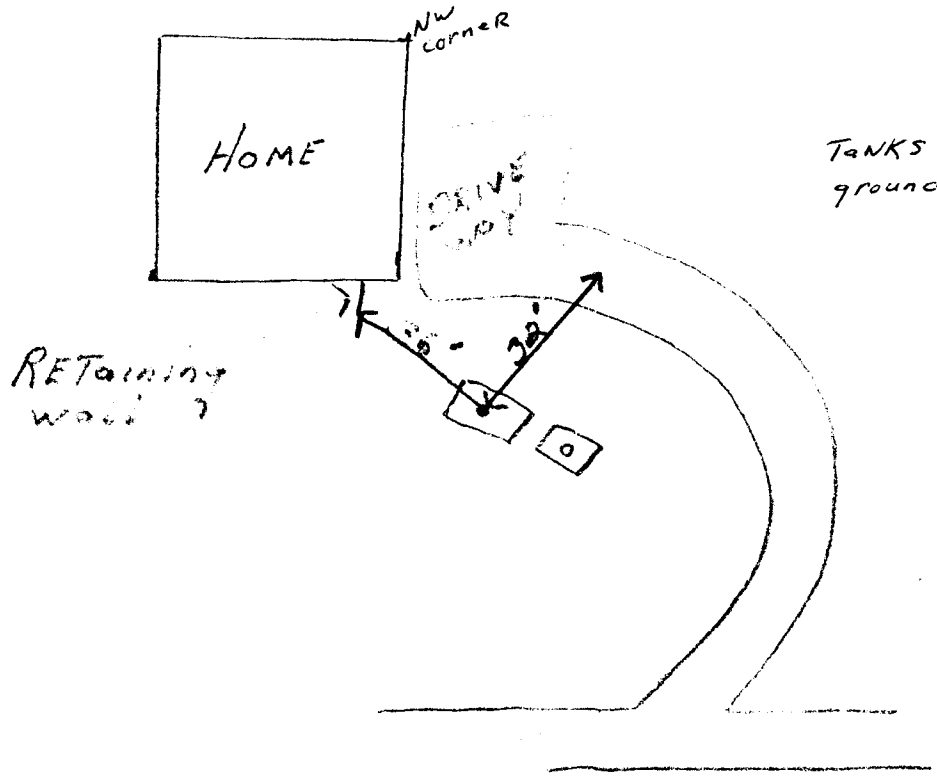

S-3
1999

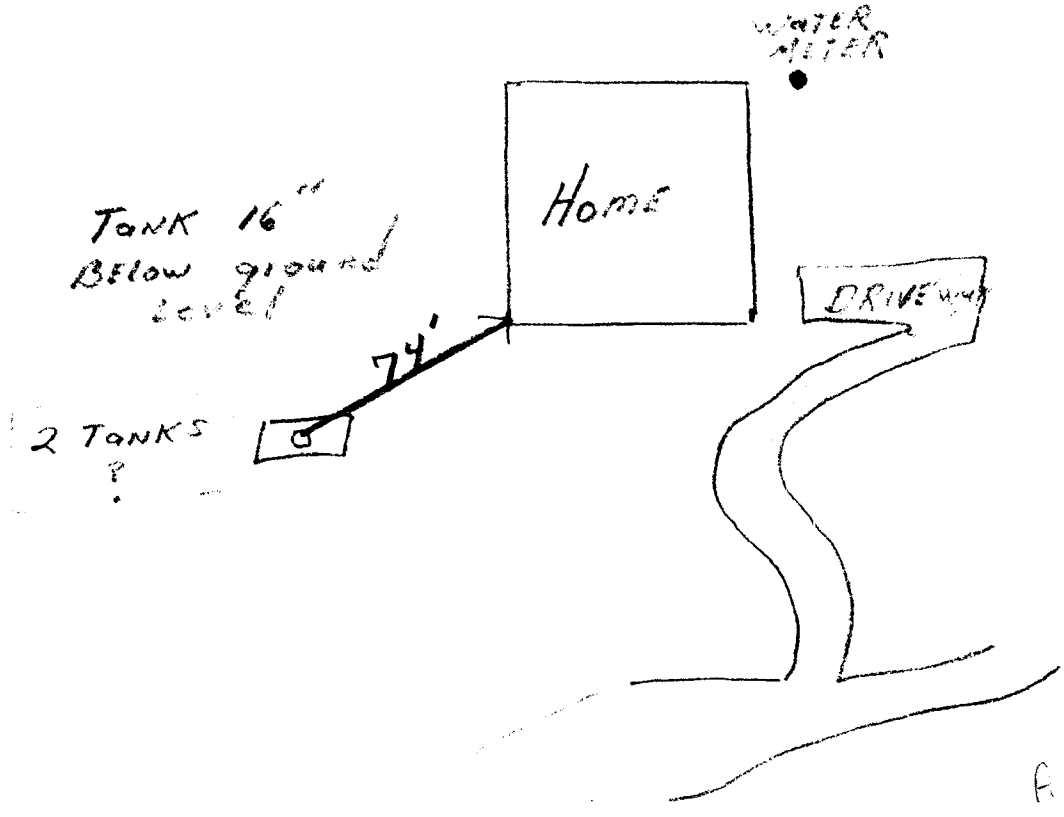

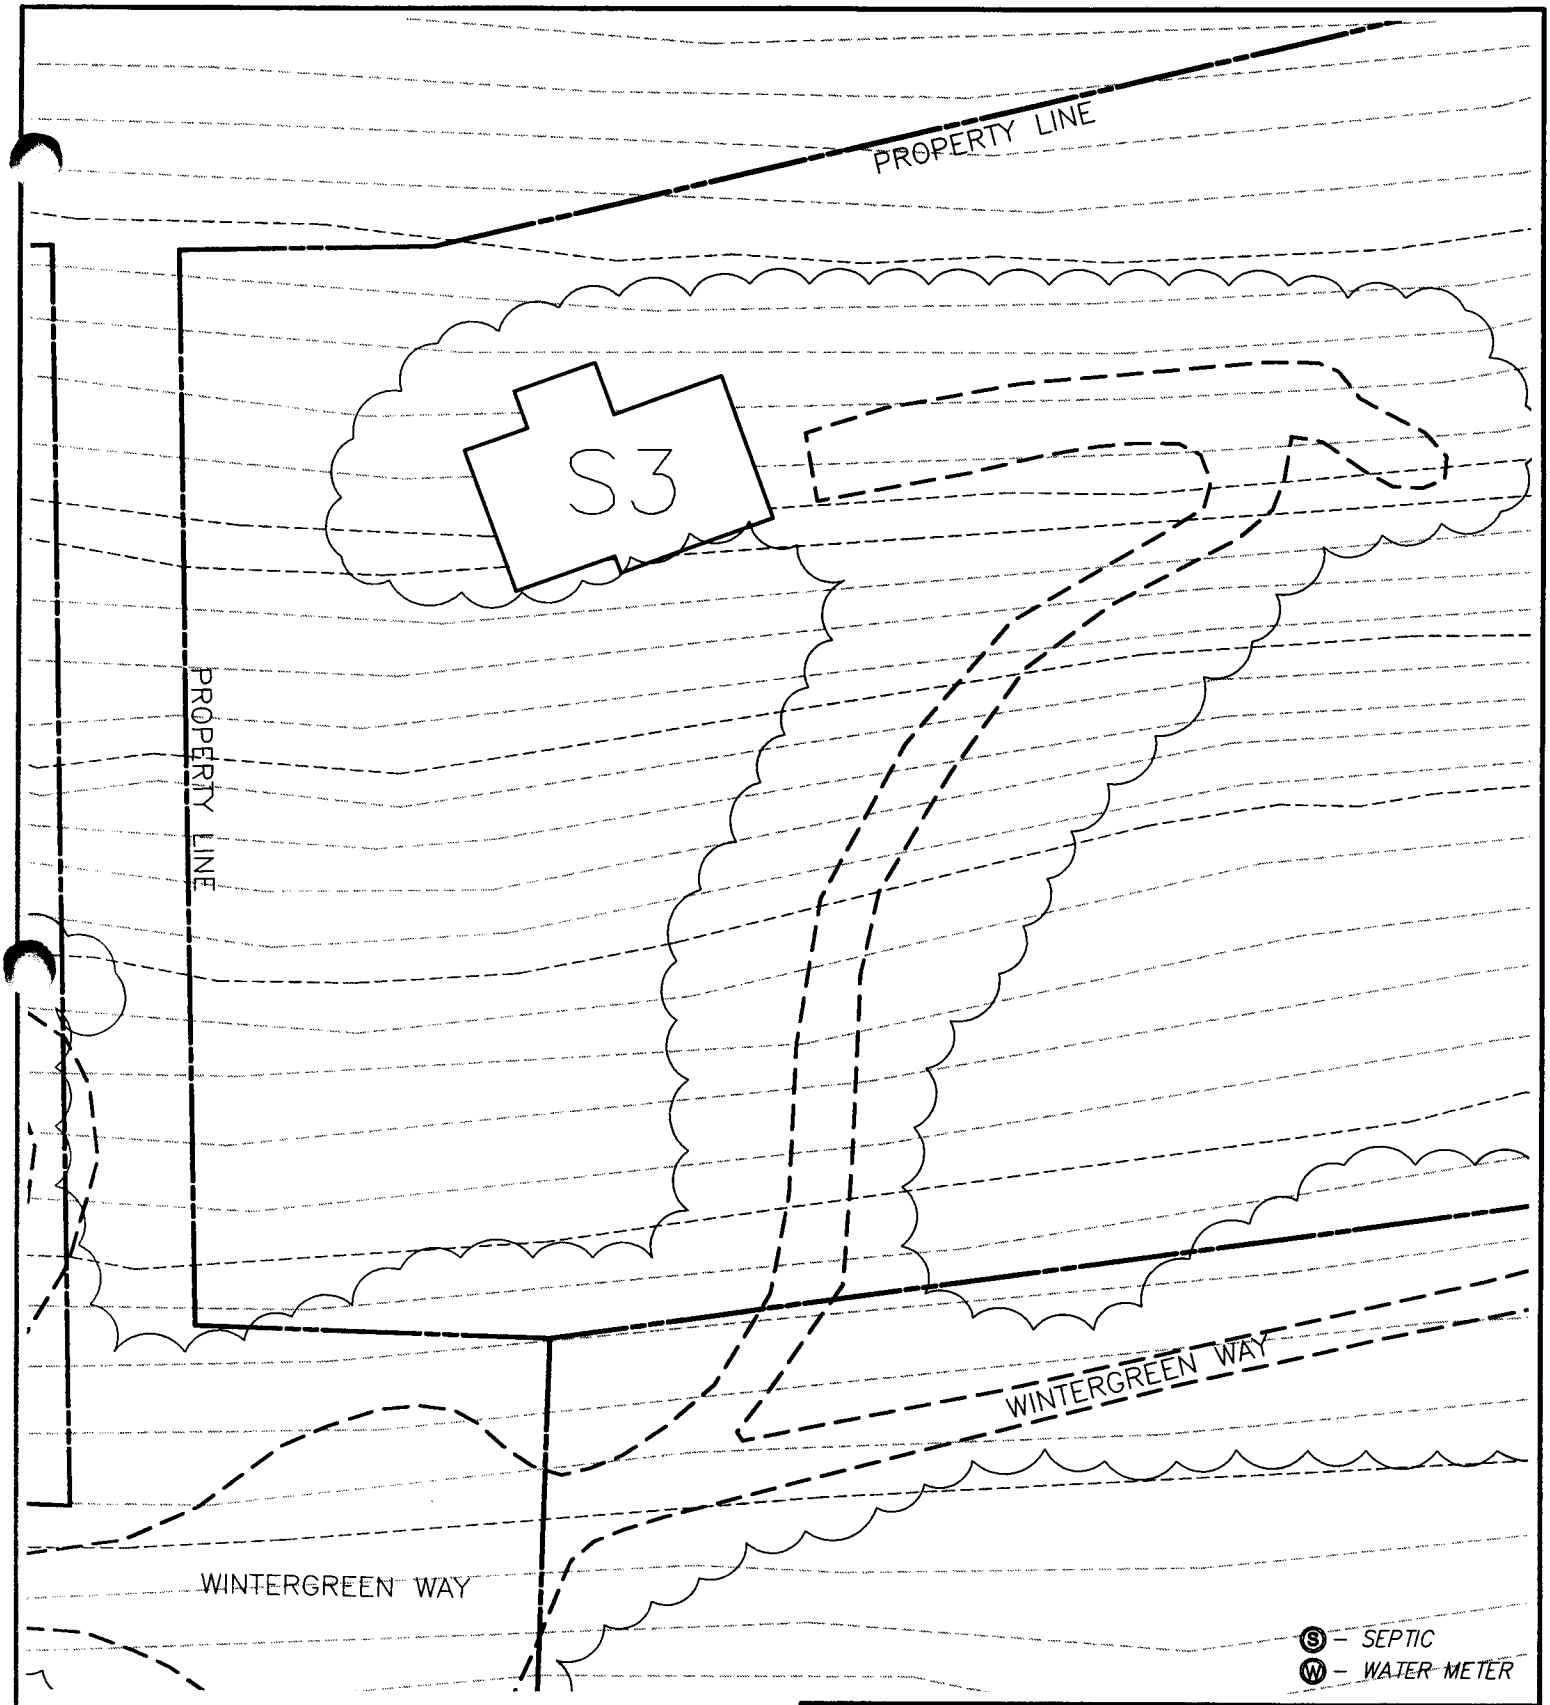

30 0 30


Scale 1" = 30 ft

NOTE:
1. Property lines and utilities are shown in an approximated location.

404 WINTERGREEN WAY SECTION S–LOT 3 UTILITY LOCATION MAP

SURVEY: PAS	C.I.: 2'
DRAWN BY: P–L	JOB NO.: 0902011
SCALE: SHOWN	DATE: 9/9/11
SHEET:	S3

C – 46

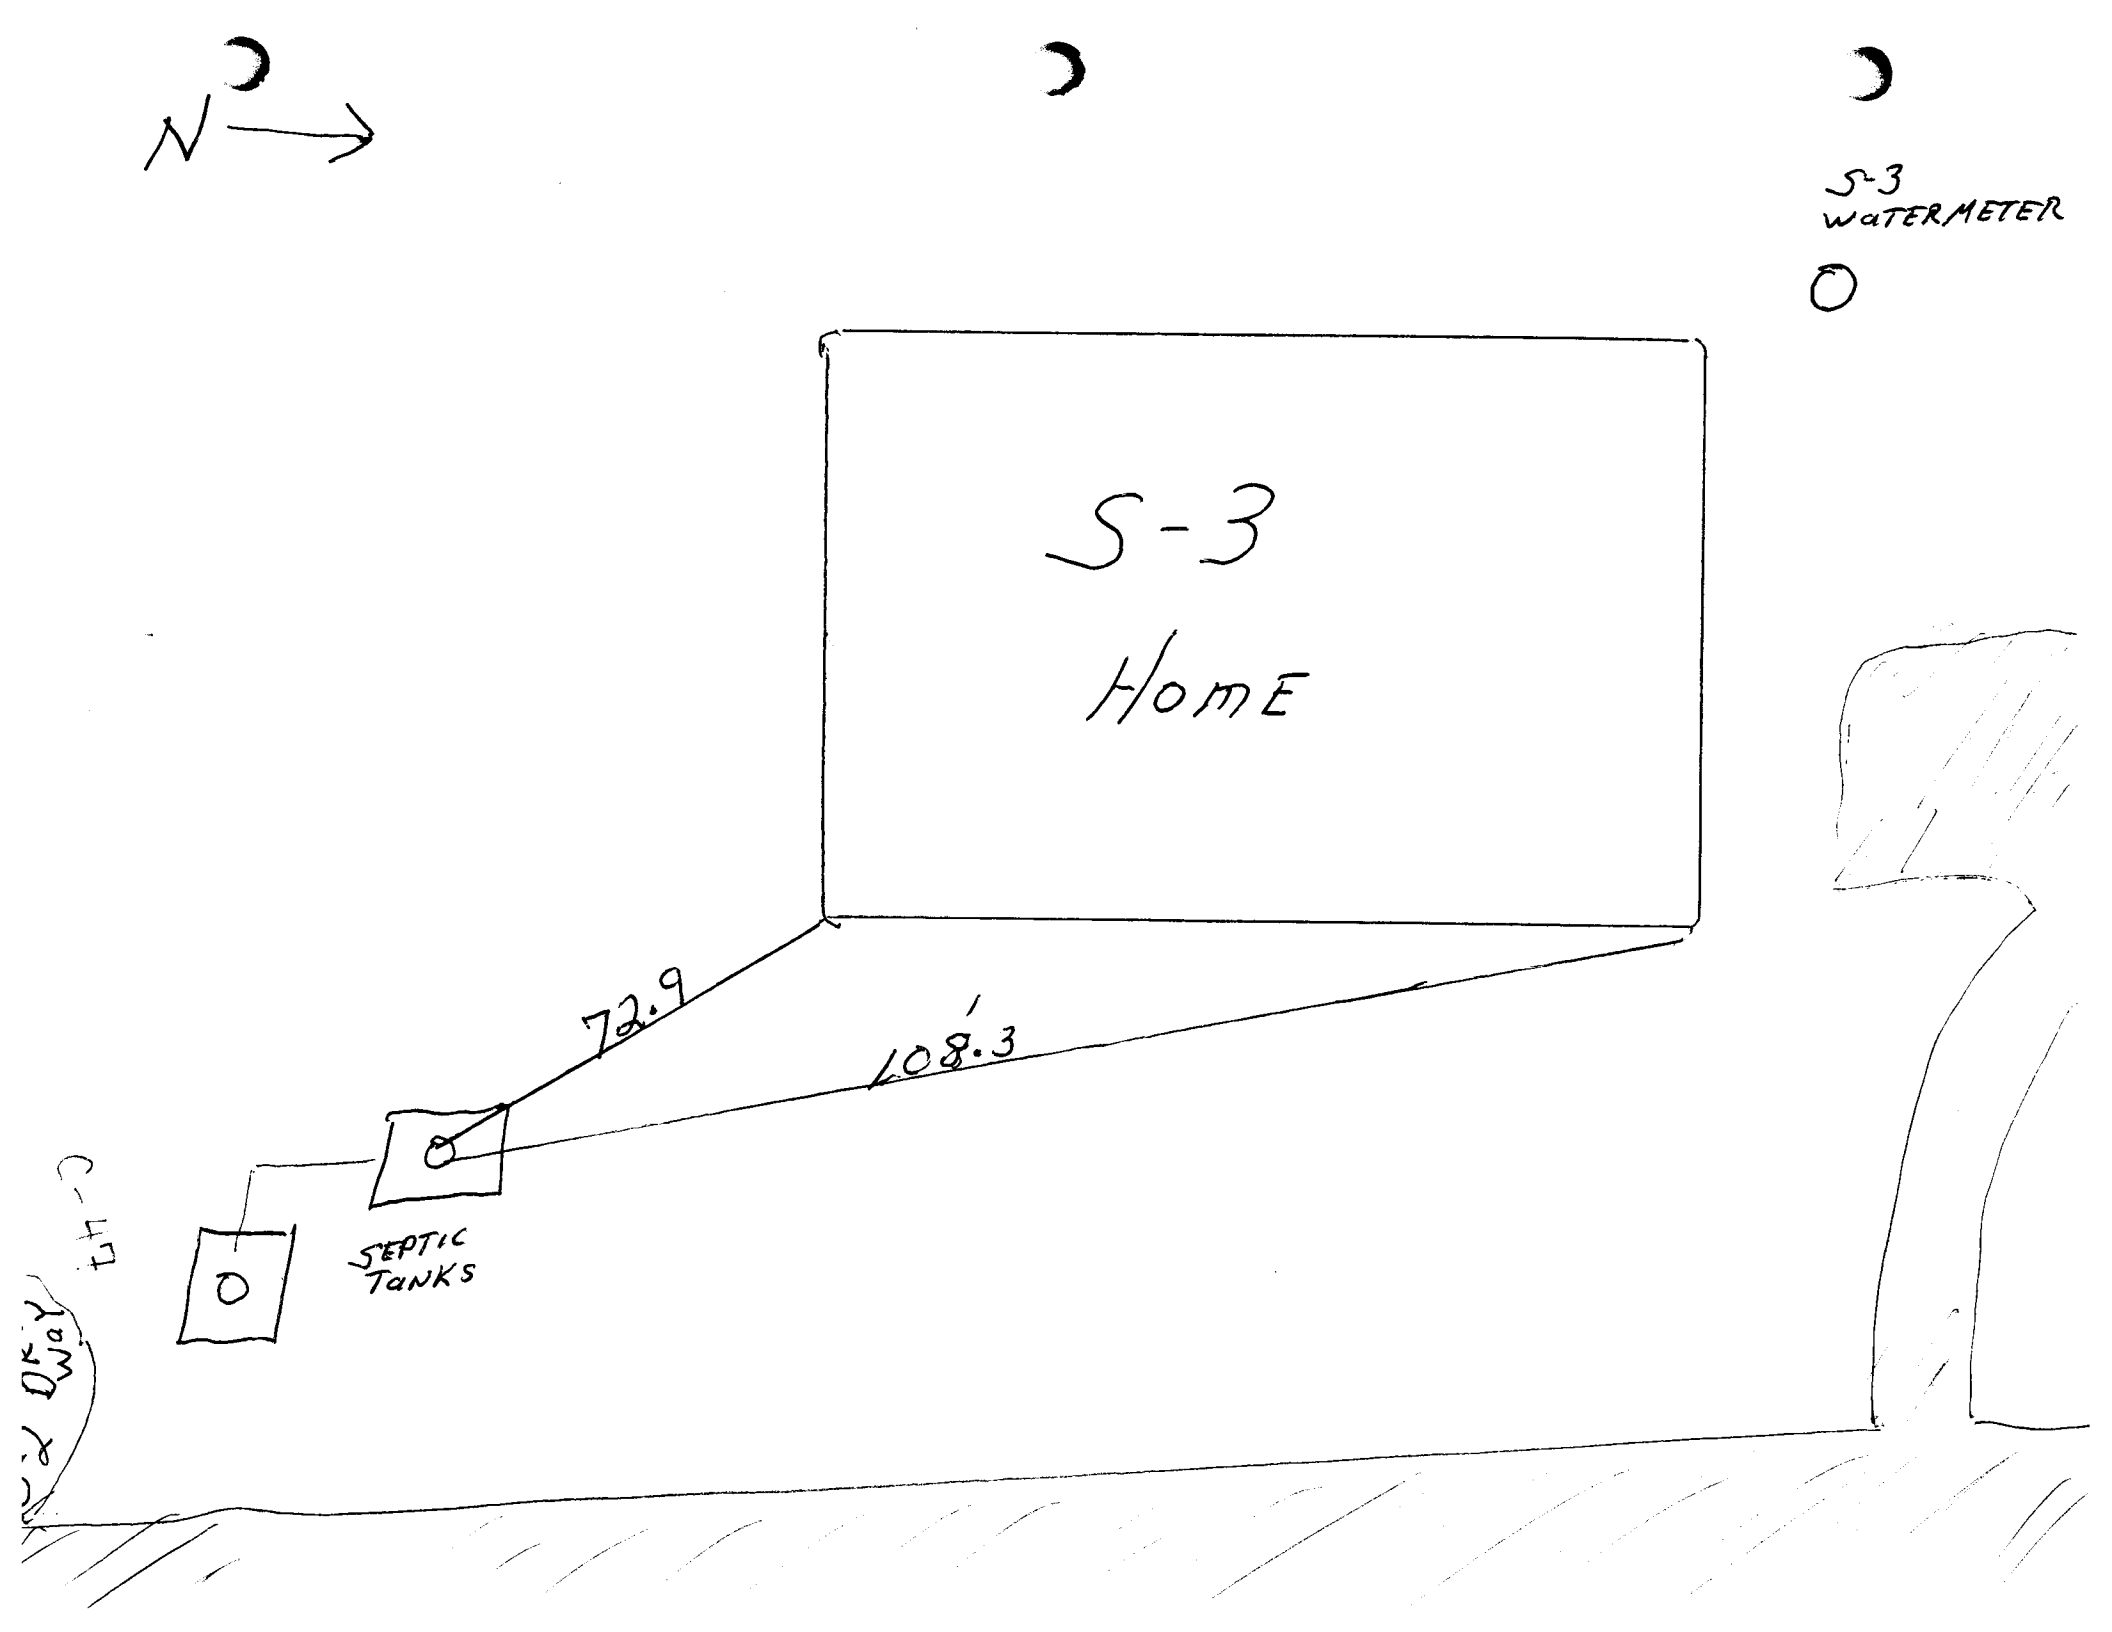
N
S-3
WATER METER
S-3
HOME
72.9'
108.3'
SEPTIC
TANKS
Way